


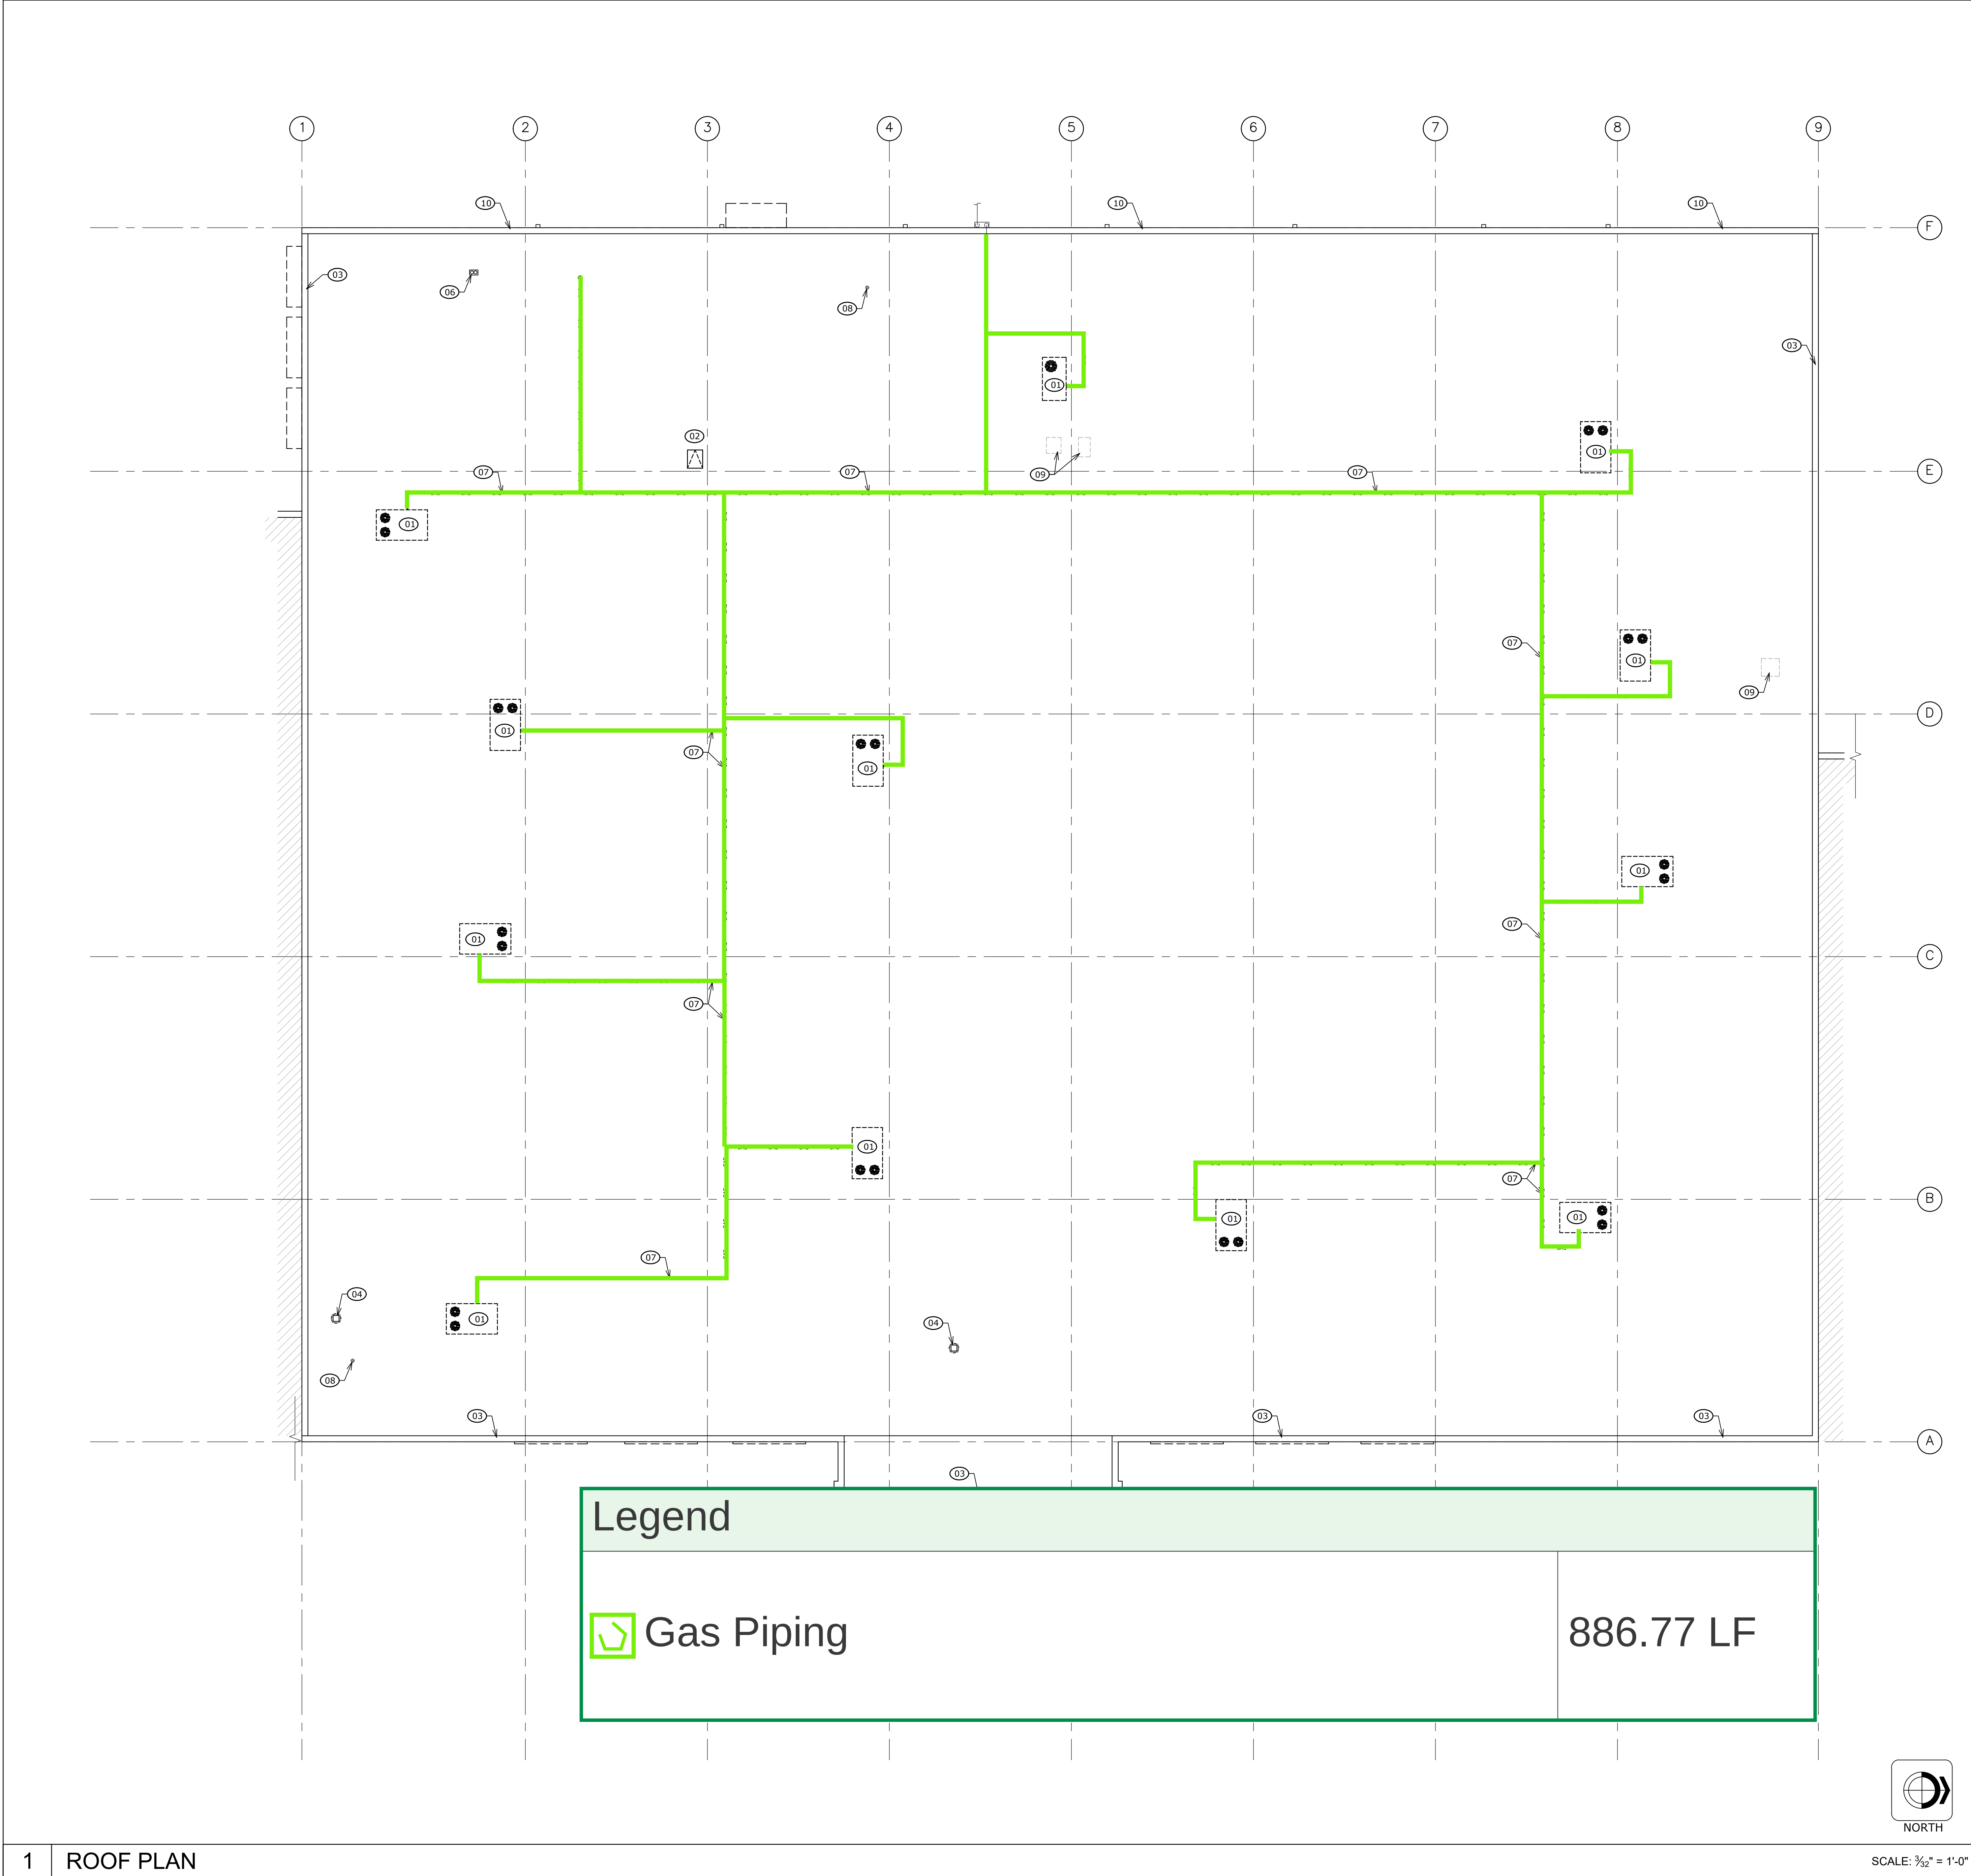


GENERAL NOTES


- 1. ROOF AND EQUIPMENT MAY BE EXISTING AND SHOWN ONLY FOR MINOR TENANT BUILD-OUT COORDINATION ONLY. THE CONTRACTOR IS RESPONSIBLE FOR BECOMING FAMILIAR WITH THE EXISTING PREMISES AND PROVIDE PRICING FOR ALL WORK QUALIFIED.
- 2. PROPOSED ROOFING MODIFICATIONS TO EXISTING ROOFING SYSTEM TO BE COMPLETED BY A QUALIFIED AND/OR APPROVED INSTALLER /ROOF CONTRACTOR. G.C. TO COORDINATE ANY LANDLORD REQUIRED ROOFING CONTRACTORS AT TIME OF BID. REGARDLESS ALL NEW ROOFING WORK SHALL BE WARRANTED AND SHALL NOT NEGATIVELY IMPACT EXISTING SYSTEMS THAT ARE TO REMAIN.
- 3. CONTRACTOR TO VERIFY & COORDINATE NEW EQUIPMENT LOCATIONS WITH M.E.P. SHEETS AND ALL EXISTING STRUCTURAL ELEMENTS. CONTACT BOBS CONSTRUCTION MANAGER WITH QUESTIONS AND VERIFICATION OF FINAL EQUIPMENT LOCATIONS.
- 4. PRE-FABRICATED CURBS SHALL BE FURNISHED AND INSTALLED BY GENERAL CONTRACTOR AND SET LEVEL. PATCH & FLASH INTO EXISTING ROOF.
- 5. NO PLUMBING VENTS OR EXHAUST UNITS WITHIN 10'-0" OF INTAKE. ADJUST AS REQUIRED TO AVOID CONFLICT.
- 6. COORDINATE ROOF CURBS WITH HVAC EQUIPMENT & INSTALL PER MANUF. SUGGESTION.
- 7. ALL ROOF OPENINGS GREATER THAN 12"x12" SHALL BE FRAMED WITH STEEL ANGLES.
- 8. MAINTAIN ALL ROOF PENETRATIONS 3'-0" OR GREATER FROM FLOW LINES.
- 9. ALL DIMENSIONS ARE FOR GENERAL ARRANGEMENT & LOCATION ONLY. ACTUAL REQUIREMENTS & DIMENSIONS SHOULD BE VERIFIED AND COORDINATED WITH EQUIPMENT, SHOP DRAWING SUBMITTALS AND STRUCTURAL FRAMING.
- 10. ALL 'NEW' EXPOSED EXTERIOR BUILDING MATERIALS TO BE U.V. RATED.
- 11. ALL CONDENSATE DRAIN CONNECTIONS, TRAPS AND PIPING TO DISCHARGE AWAY FROM UNITS. DISCHARGE TO DRAIN ONTO SPLASH BLOCKS, TYPICAL.
- 12. REFER TO SHEET D1.0 FOR ADDITIONAL DEMOLITION REQUIRED ON ROOF.
- 13. ALL REMOVED ROOF EQUIPMENT SHALL BE FULLY PATCHED TO MATCH EXISTING ROOFING SYSTEM.
- 14. PROVIDE CRICKET INSULATION AROUND EQUIPMENT CURBS TO PROVIDE PROPER DRAINAGE AROUND EQUIPMENT.
- 15. ALL EQUIPMENT SUPPORTED BY CURBS SHALL BE MECHANICALLY ATTACHED TO CURBS. CURBS MUST BE MECHANICALLY ATTACHED TO STRUCTURE. NO GRAVITY CONNECTIONS. REFER TO ELECTRICAL DRAWINGS FOR ADDITIONAL ROOF PENETRATIONS.
- 16. GC IS TO INCLUDE IN THE BASE CONTRACT SCOPE TO REMOVE ALL PRIOR TENANT IMPROVEMENTS THAT ARE NOT SPECIFICALLY CALLED OUT IN THESE DRAWINGS TO BE REUSED, AND PATCH BACK TO THE ORIGINAL ADJACENT FINISH FINISH CONDITIONS WHETHER KEY NOTED SPECIFICALLY OR NOT.

ROOF KEYNOTES


- 01 NEW ROOF TOP HVAC UNIT IN EXISTING LOCATION. SEE MECH DRAWINGS.
- 02 NEW ROOF HATCH AND LADDER. RE: A8.2 FOR DETAILS.
- 03 EXISTING PARAPET W/ ALUMINUM COPING/D RIP EDGE TYPICAL.
- 04 NEW EXHAUST FAN AND CURB. RE: DETAIL THIS SHEET.
- 05 NOT USED
- 06 NEW COMBINATION/FLUE OUTSIDE AIR INTAKE FOR UNIT HEATER. RE: MECHANICAL
- 07 ALL GAS PIPING TO BE PREPPED AND PAINTED YELLOW. RE: P2.0.
- 08 VENT RISER, RE: DETAILS THIS SHEET, PLUMBING PLANS.
- 09 REMOVE ROOF EQUIPMENT INCLUDING CURBS, INFILL METAL DECK, INSULATION, AND ROOFING MEMBRANE TO MATCH EXISTING CONSTRUCTION.
- 10 EXISTING ALUMINUM GUTTER SYSTEM, NO CHANGE.

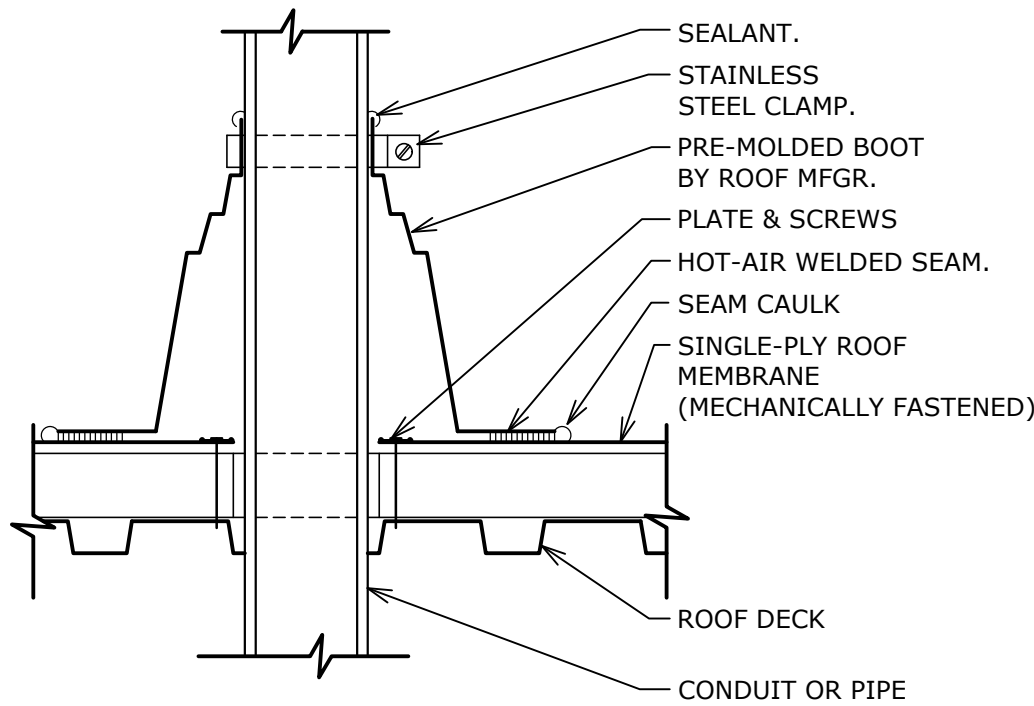

2 VENT PIPE DETAIL SCALE: 1" = 1'-0"

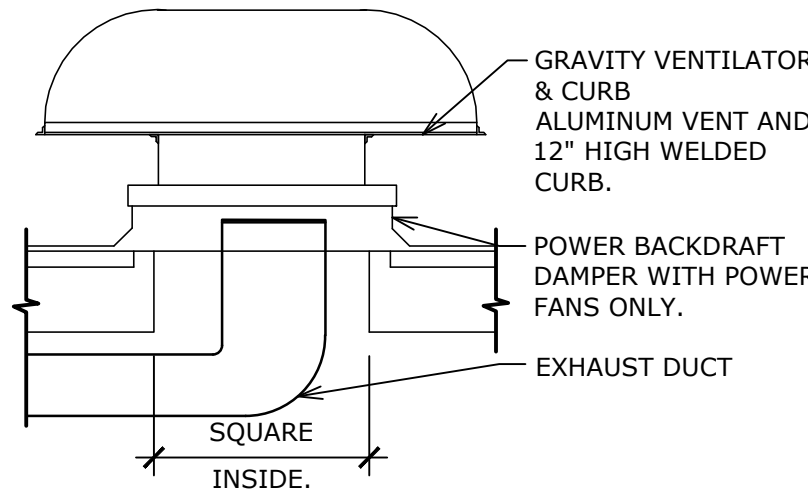

3 EXHAUST HOOD DETAIL SCALE: 1" = 1'-0"

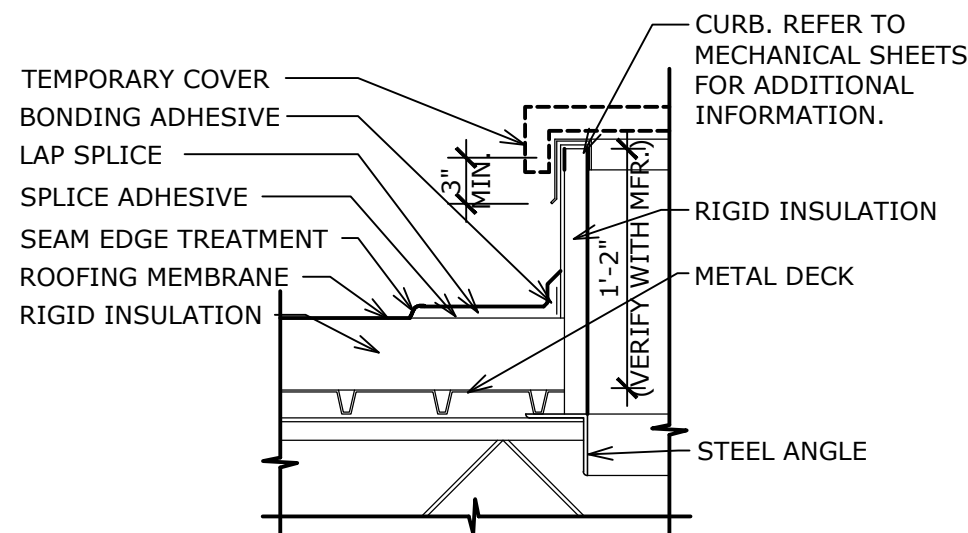

4 CURB DETAIL SCALE: 1" = 1'-0"

CERTIFICATION:



CAMBURAS & THEODORE, LTD
ARCHITECTURE | ENGINEERING | INTERIORS
2454 E. Dempster St. Suite 202
Des Plaines, IL 60016
P (847) 298-1525 | F (847) 350-6130
www.camburasandtheodore.com

THESE DRAWINGS AND SPECIFICATIONS, AS INSTRUMENTS OF SERVICE, ARE AND SHALL REMAIN THE PROPERTY OF THE ARCHITECT. WHETHER THE PROJECT FOR WHICH THEY ARE MADE IS EXECUTED OR NOT, THESE DRAWINGS AND SPECIFICATIONS SHALL NOT BE USED BY ANY PERSON OR ENTITY FOR ANY PURPOSE OTHER THAN THAT AUTHORIZED BY THE ARCHITECT. ANY REUSE OR MODIFICATION OF THESE DRAWINGS OR SPECIFICATIONS WITHOUT THE WRITTEN CONSENT OF C + T LTD. Copyright © 2025

BOB'S Discount Furniture.
COBB PLACE SHOPPING CENTER
840 ERNEST W BARRETT PARKWAY NW, SUITE 250
KENNESAW, GA 30144

REVISION DATES

NO	DATE	TYPE

ISSUE DATES

TYPE	DATE
PERMIT/CONSTRUCTION SET	05/01/26

DRAWN BY

CHECKED BY

PROJECT NUMBER

25-91018

DATE

05/01/2026

SHEET TITLE

ROOF PLAN

SHEET NUMBER


A3.0

1 ROOF PLAN

SCALE: 3/32" = 1'-0"

DOOR SCHEDULE

EXIST DOOR	NO.	TYPICAL LOCATION	TYPICAL DOOR SIZE			TYPE	MATERIAL	VISION LITE	LABEL	FRAME	HARDWARE		REMARKS
			W	H	T					MAT'L.	SET	KEY	
	001A	VESTIBULE	14'-0"	7'-6"		8	ALUM. & 1" INSULATED GLASS	Y	---	ALUM.	**	Y	ASSA ABLOY AUTOMATIC (SL500) SLIDING DOOR SYSTEM WITH FULL BREAKOUT EGRESS SYSTEM. **INSTALL EXTERIOR VESTIBULE HARDWARE AND LOCKSET PER MANF. RECOMMENDATIONS.
	001B	VESTIBULE	14'-0"	7'-6"		8	ALUM. & GLASS	Y	---	ALUM.	**	Y	ASSA ABLOY AUTOMATIC (SL500) SLIDING DOOR SYSTEM WITH FULL BREAKOUT EGRESS SYSTEM. **INSTALL INTERIOR VESTIBULE HARDWARE AND LOCKSET PER MANF. RECOMMENDATIONS.
	002	DINING	3'-0"	7'-0"	1-3/4"	3	HM-STI		---	HM	6A	Y	
	004A	BEDROOMS	3'-0"	7'-0"	1-3/4"	3	HM-STI		---	HM	6A	Y	
	004B	BEDROOMS	3'-0"	7'-0"	1-3/4"	3	HM-STI		---	HM	6A	Y	4" TOP FRAME
	005	KIDS	3'-0"	7'-0"	1-3/4"	3	HM-STI		---	HM	6A	Y	4" TOP FRAME
	008	MANAGER/COUNT	3'-0"	7'-0"	1-3/4"	2	S.C. WOOD & GLASS	Y	---	HM	1A	Y	TRILOGY T2 LOCKSET
	009	BREAKROOM	3'-6"	7'-0"	1-3/4"	2	S.C. WOOD & GLASS	Y	---	HM	3		
	010	DATA	3'-0"	7'-0"	1-3/4"	1	S.C. WOOD		---	HM	2A	Y	
	013	UNISEX	3'-0"	7'-0"	1-3/4"	1	S.C. WOOD		---	HM	4	Y	UNDERCUT DOOR 1"
	014	UNISEX	3'-0"	7'-0"	1-3/4"	1	S.C. WOOD		---	HM	4	Y	UNDERCUT DOOR 1"
	015	JANITOR	3'-0"	7'-0"	1-3/4"	1	S.C. WOOD		---	HM	2A	Y	UNDERCUT DOOR 1"
	016A	RECEIVING	(2)3'-0"	7'-0"	1-3/4"	5	*	Y	---		MFG		*ELIASON DOORS, MODEL P-11 PLUS, COLOR: GREY. DOUBLE-ACTING PUSH HARDWARE - NO LOCKSET! INSTALL S.S. KICK PLATE FROM FLOOR TO UNDERSIDE OF VISION LITE. 2" FRAME ON TOP. ORDER DOOR WITH JAMB GUARDS. -PROVIDE SIGNAGE "NOT AN EXIT" - OR AS DIRECTED BY FIRE OFFICIAL.
	016B	CUSTOMER PICKUP	8'-0" VIF	8'-0" VIF	---	6	*	Y	---	---	---		WAYNE DALTON THERMOSPAN 150 INSULATED SECTION OVERHEAD WITH VISION LITE AND 25,000 CYCLE SPRING NO POWER OPENER WITH SINGLE VISION LITE, STEP DOWN BRACKET, AND SLIDE BOLT WITH HOLE FOR PAD LOCK.
	016C	REVEIVING	3'-0"	7'-0"	1-3/4"	3	HM-STI		---	HM	6A	Y	4" TOP FRAME
	016D	LOADING/UNPACKING	8'-0" VIF	8'-0" VIF	---	6	*	Y	---	---	---		WAYNE DALTON THERMOSPAN 150 INSULATED SECTION OVERHEAD WITH VISION LITE AND 25,000 CYCLE SPRING NO POWER OPENER WITH SINGLE VISION LITE, STEP DOWN BRACKET, AND SLIDE BOLT WITH HOLE FOR PAD LOCK.
	016E	LOADING/UNPACKING	8'-0" VIF	8'-0" VIF	---	6	*	Y	---	---	---		WAYNE DALTON THERMOSPAN 150 INSULATED SECTION OVERHEAD WITH VISION LITE AND 25,000 CYCLE SPRING NO POWER OPENER WITH SINGLE VISION LITE, STEP DOWN BRACKET, AND SLIDE BOLT WITH HOLE FOR PAD LOCK.
	016F	LOADING/UNPACKING	8'-0" VIF	8'-0" VIF	---	6	*	Y	---	---	---		WAYNE DALTON THERMOSPAN 150 INSULATED SECTION OVERHEAD WITH VISION LITE AND 25,000 CYCLE SPRING NO POWER OPENER WITH SINGLE VISION LITE, STEP DOWN BRACKET, AND SLIDE BOLT WITH HOLE FOR PAD LOCK.
	017	SPRINKLER ROOM	3'-0"	7'-0"	1-3/4"	1	S.C. WOOD		---	HM	2A	Y	

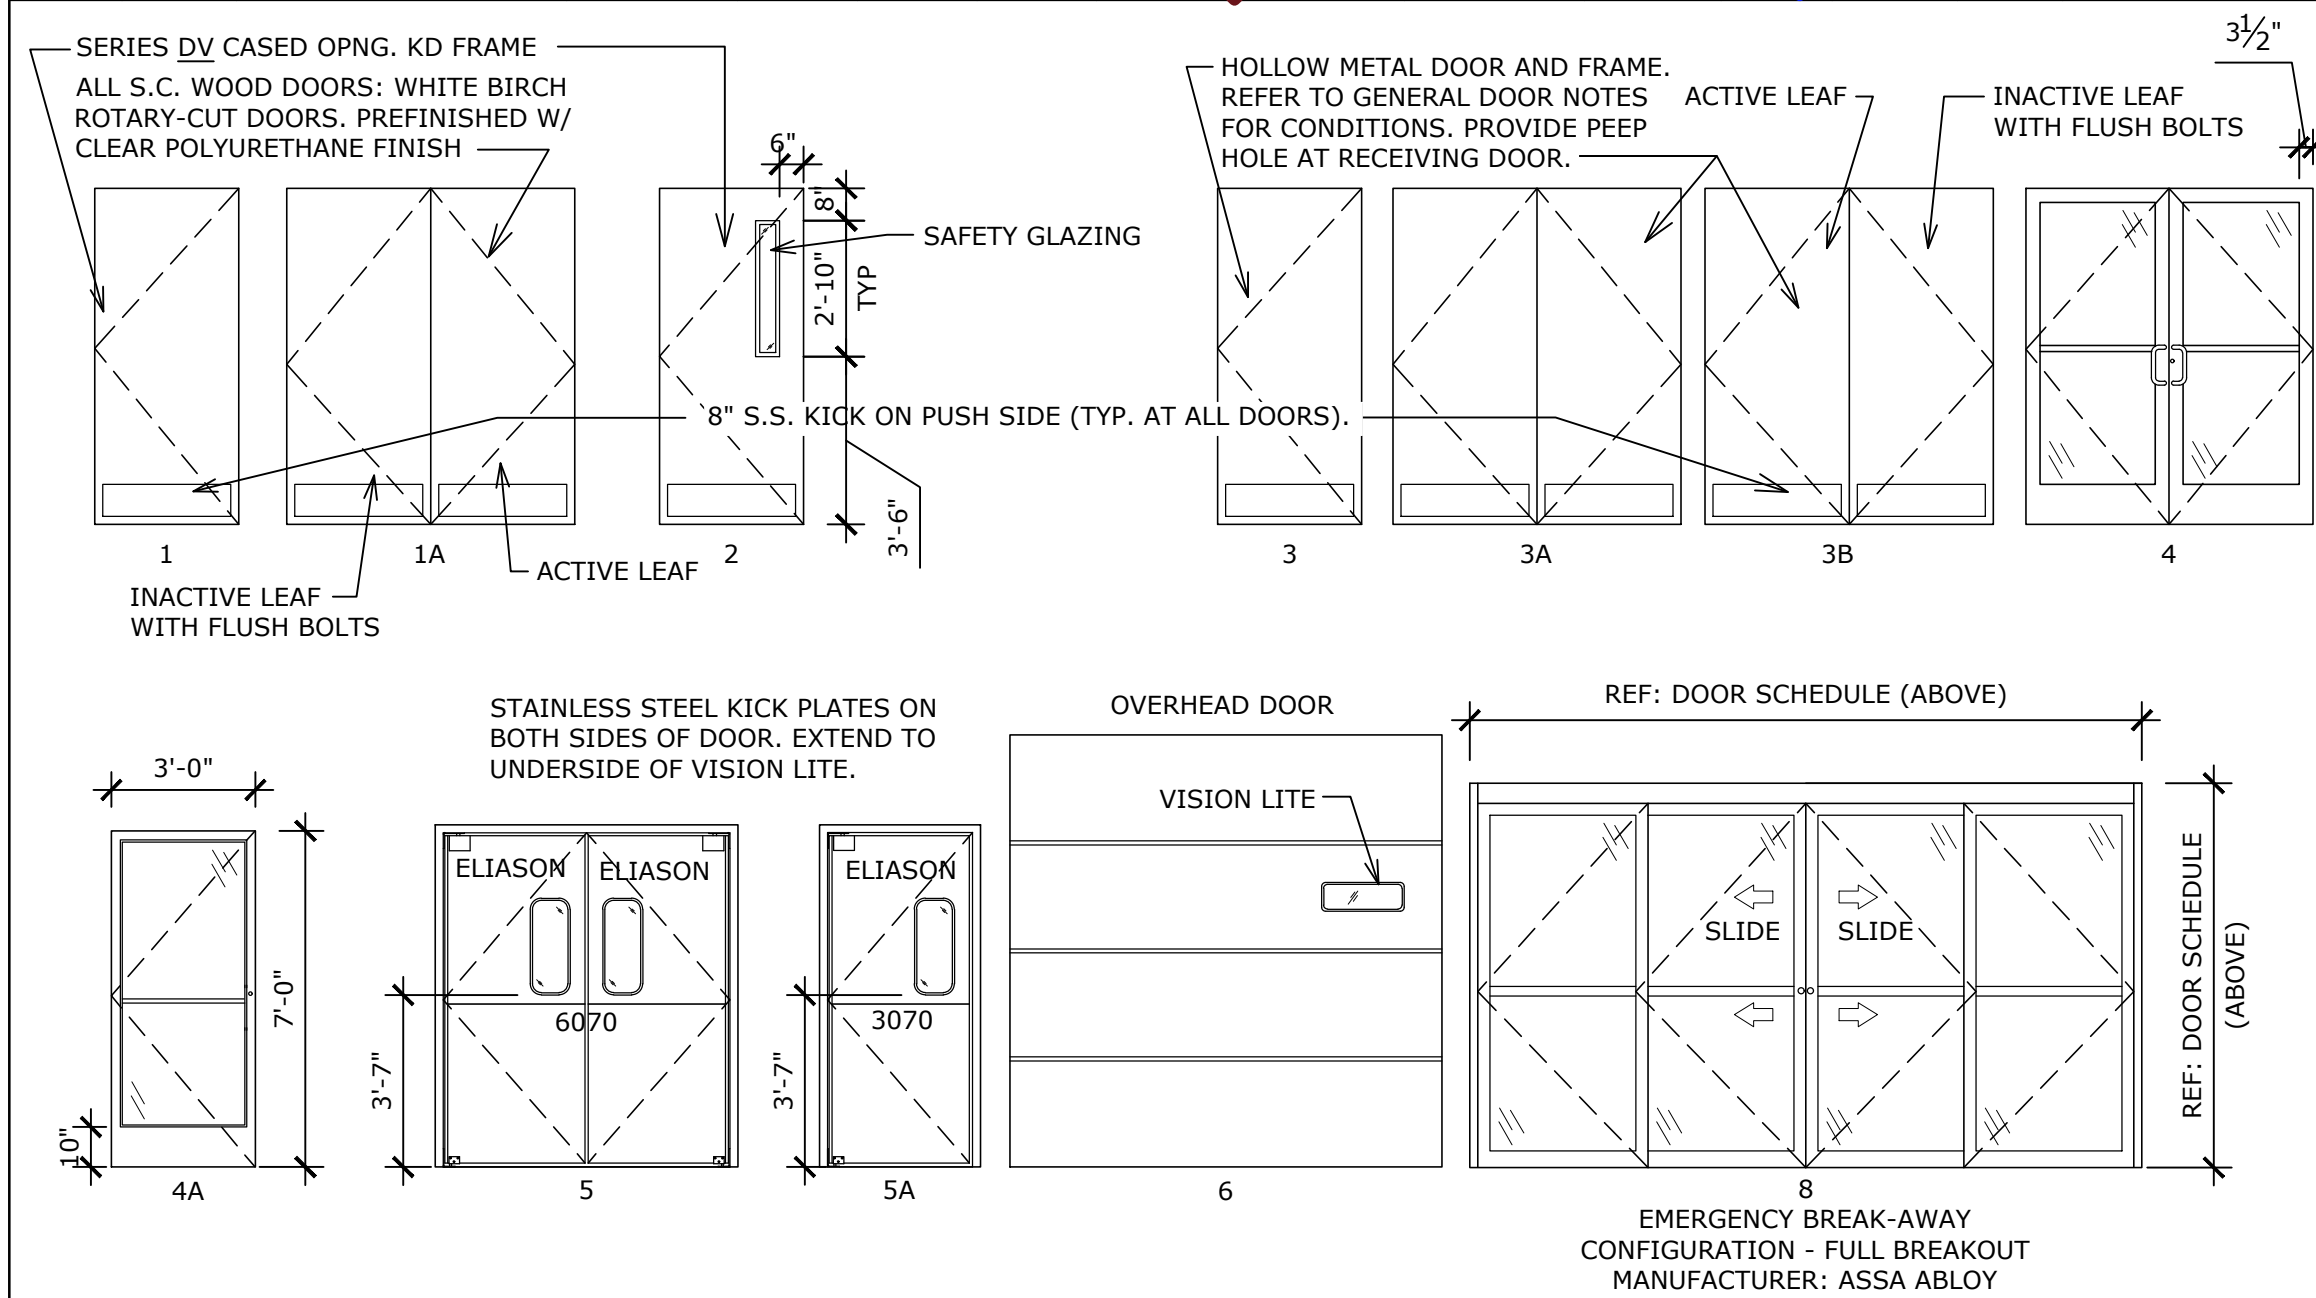

DOOR GENERAL NOTES

1. EXIT DOORS USED IN PAIRS SHALL BE EQUIPPED WITH AUTOMATIC FLUSH BOLTS. MANUALLY OPERATED EDGE BOLTS OR MANUAL SURFACE MOUNTED BOLTS ARE PROHIBITED. THE DOOR LEAF HAVING THE AUTOMATIC FLUSH BOLTS SHALL HAVE NO HARDWARE ON THE EXTERIOR FACE. THE UNLATCHING OF ANY LEAF SHALL NOT REQUIRE MORE THAN ONE OPERATION AND AT LEAST ONE OF THE DOORS SHALL HAVE AN EASY REAR AND FRONT HANDLE.
2. THE FLOOR OR LANDING SHALL NOT BE MORE THAN 1/2" LOWER THAN THE TOP OF THE THRESHOLD OF THE DOOR. CHANGE IN LEVEL BETWEEN 1/4" AND 1/2" SHALL BE BEVELED WITH A GRADIENT NO GREATER THAN 1:2.
3. TYPICAL FOR ALL INTERIOR WOOD ELEMENTS, ALL COMPOSITE WOOD SUBSTRATES SHALL BE "NO ADDED URSA FORMALDEHYDE (NAUF) FOR ALL WOOD INSIDE THE WATERPROOF MEMBRANE OF THE BUILDING.
4. ALL EXTERIOR STEEL DOOR FRAMES SHALL BE WELDED. ALL INTERIOR DOOR FRAMES SHALL BE BOLTED.
5. EXTERIOR METAL DOORS SHALL HAVE PANIC BARS FOR EGRESS AND EXTERIOR DOOR HANDLE ONLY FOR SECURING THE DOOR (PULLING IT CLOSED).
6. ALL EXISTING METAL DOORS & DOOR FRAMES TO BE REPLACED (UNO).

SLIDING DOOR NOTES

NOTES


1. ELECTRICAL REQUIREMENTS: BY ELECTRICAL CONTRACTOR
 - 120 VAC, 15/20 AMP MIN TO POWER OPERATOR
 - CONTROL CIRCUIT FROM SECURE ACTIVATION TO OPERATOR
2. ROUGH OPENING SHALL PROVIDE 1/4"[6] SHIM SPACE ON SIDES AND TOP OF PACKAGE.
3. LIMITS OF ACTIVATION AND SAFETY ZONES ARE FOR REFERENCE ONLY; SEE ANSI/BHMA A156.10 FOR DETAILED REQUIREMENTS.
4. SEE MANUFACTURER SPECIFICATIONS FOR ADDITIONAL INFORMATION.

HARDWARE SCHEDULE

HARDWARE SET #1 - INTERIOR WOOD SINGLE DOOR (MANAGERS/COUNT ROOM, OFFICE): ENTRANCE FUNCTION (each opening to receive):						
QTY	PART	MANUFACTURER	PART #	FINISH	SPECIAL INSTRUCTIONS	
3 EA	HINGES:	MC KINNEY	MP/B79 (US260) 4.5" X 4.5"	626 (Satin Chromium), US260	3 HINGES PER DOOR.	
1 EA (VERIFY - SEE SPECIAL INSTRUCTION N)	LOCKSET (OPTION - 1A):	ALARM LOCK SYSTEMS	TRILGY12 - DL2700C/260	626 (Satin Chromium), US260	MANAGERS/COUNT ROOM ONLY: TRILGY LOCKSET. CONTRACTOR IS TO INSTALL WITH A RED COLORED TEMPORARY INSTA KEY 7 PIN REMOVABLE CORE AND CORE CHANGING KEY.	
1 EA (VERIFY - SEE SPECIAL INSTRUCTION N)	LOCKSET (OPTION - 1B):	ACCENTRA (YALE)	9-PB9407IN-626	626 (Satin Chromium), US260	OFFICE ONLY: ENTRANCE FUNCTION - WITH A RED COLORED TEMPORARY INSTA KEY 7 PIN REMOVABLE CORE AND CORE CHANGING KEY.	
1 EA	IC CORE:	INSTANEY	SPIC CORE 7 PIN		RED COLORED	
1 EA	CLOSER:	CORBIN-RUSSWIN (CR)	(CR) DC6200	689 (Painted Silver)	FASTEN CLOSER BODY TO DOOR ON SWING SIDE OF DOOR WITH WOOD SCREWS (NO EX BOLTS OR PARALLEL BAR) AND JUST TO NO MORE THAN 12 INBS PULL RESISTANCE (EASY OPENING AND SLOW CLOSING).	
1 EA	KICKPLATE:	ASSA ABLOY-ROCKWOOD	K1050 US320D 12 34 BEV	630 (Satin SS), US320	ATTACHED TO THE PUSH SIDE OF THE DOOR 1/2" ABOVE THE BOTTOM, AND IN 1" FROM BOTH RIGHT AND LEFT EDGES THE DOOR.	
1 EA	WALL STOP:	ASSA ABLOY-ROCKWOOD	400	626 (Satin Chromium), US260	MOUNTED ON THE LATCH SIDE OF THE DOOR. LATCH AND INSTALL 1/4" CLEAR WIRE GLASS AND USE GLAZING TAPE TO PROTECT GLASS IN THE FRAME.	
1 EA	VISION LITE:	NATIONAL GUARD PRODUCTS (NGP)	L-FRA100-WG-G138 6x36 TAN	TAN - THEN FIELD PAINT WITH RUST-OLEAN SPRAY PAINT #7721380 - "SILVER METALLIC"	BEHIND DRYWALL AT DOOR BUMPER INSTALL 2X10 SOLID WOOD BACKING SQUARELY SECURED INTO THE WALL.	
1 SET	SMOKE SEAL:	ASSA ABLOY - PEMKO	HSS2000x188BL	BLACK (BL)	INSTALL AFTER FRAME IS PAINTED	
HARDWARE SET #2 - INTERIOR WOOD SINGLE DOOR (DATA, ELECTRICAL, RISER, JANITORS, STORAGE) - STORE ROOM FUNCTION (each opening to receive):						
QTY	PART	MANUFACTURER	PART #	FINISH	SPECIAL INSTRUCTIONS	
3 EA	HINGES:	MC KINNEY	MP/B79 (US260) 4.5" X 4.5"	626 (Satin Chromium), US260	3 HINGES PER DOOR	
1 EA (VERIFY - SEE SPECIAL INSTRUCTION N)	LOCKSET (OPTION - 2A):	ASSA ABLOY ACCENTRA (YALE)	9-PB9405IN-626	626 (Satin Chromium), US260	STORE ROOM FUNCTION - WITH A RED COLORED TEMPORARY INSTA KEY 7 PIN REMOVABLE CORE AND CORE CHANGING KEY.	
1 EA (VERIFY - SEE SPECIAL INSTRUCTION N)	EXIT DEVICE (OPTION - 2B):	ALLEGION - VON DUPRIN WITH SEPARATE INSTANEY CORE CYLINDER	22-LX 230L 06-SP2B-3"	SP2B (Aluminum Paint)	** WHEN REQUIRED BY CITY AT INTERIOR ELECTRICAL ROOM DOOR ONLY** CONTRACTOR TO SUPPLY/INSTALL A RED COLORED TEMPORARY INSTA KEY 7 PIN REMOVABLE CORE AND CORE CHANGING KEY IN THE LEVER SIDE OF THE DOOR.	
1 EA (VERIFY - SEE SPECIAL INSTRUCTION N)	IC CORE:	INSTANEY	SPIC CORE 7 PIN	626 (Satin Chromium), US260	**WHEN OPTION 2A & 2B - VON DUPRIN 22 PANIC DEVICE IS REQUIRED ONLY** A RED COLORED TEMPORARY INSTA KEY 7-PIN REMOVABLE CORE AND CORE CHANGING KEY AND CHANGING RINGS STRAIGHT CAN BE USED.	
1 EA	KICKPLATE:	ASSA ABLOY-ROCKWOOD	K1050 US320 12 34 BEV	630 (Satin SS), US320	ATTACHED TO THE PUSH SIDE OF THE DOOR 1/2" ABOVE THE BOTTOM, AND IN 1" FROM BOTH RIGHT AND LEFT EDGES THE DOOR.	
1 EA	WALL STOP:	ASSA ABLOY-ROCKWOOD	400	626 (Satin Chromium), US260	PROVIDE BACKING IN WALL.	
3 EA	SILENCERS:	ASSA ABLOY-ROCKWOOD	608-RKW	GREY	INSTALL AFTER FRAME IS PAINTED	
HARDWARE SET #3 - INTERIOR WOOD SINGLE DOOR (BREAKROOM [3'-6" wide door], MULTI-USER RESTROOM [3'-6" wide door]) - PUSH PULL HARDWARE (each opening to receive):						
QTY	PART	MANUFACTURER	PART #	FINISH	SPECIAL INSTRUCTIONS	
3 EA	HINGES:	MC KINNEY	MP/B79 (US260) 4.5" X 4.5"	626 (Satin Chromium), US260	STANDARD DUTY BALL BEARING MORTISE HINGE	
1 EA	PULL:	ASSA ABLOY-ROCKWOOD	107-X-70C	630 (Satin Stainless Steel), US320	COUNTERSINK THE PULL BAR THROUGH BOLT SO PUSH PLATE ON THE OTHER SIDE OF DOOR COVERS OVER THE THROUGH BOLTS.	
1 EA	PUSH:	ASSA ABLOY-ROCKWOOD	71C	630 (Satin Stainless Steel), US320	MOUNT AFTER THE PULL IS INSTALLED TO COVER THE RECESSED PULL BAR THROUGH BOLTS.	
1 EA	CLOSER:	CORBIN-RUSSWIN (CR)	(CR) DC6200	689 (Painted Silver)	FASTEN CLOSER BODY TO DOOR ON SWING SIDE OF DOOR WITH WOOD SCREWS (NO EX BOLTS OR PARALLEL BAR) AND JUST TO NO MORE THAN 12 INBS PULL RESISTANCE (EASY OPENING AND SLOW CLOSING).	
1 EA (BREAKROOM ONLY)	VISION LITE:	NATIONAL GUARD PRODUCTS (NGP)	L-FRA100-WG-G138 6x36 TAN	TAN - THEN FIELD PAINT WITH RUST-OLEAN SPRAY PAINT #7721380 - "SILVER METALLIC"	**BREAKROOM ONLY** MOUNTED ON THE LATCH SIDE OF THE DOOR. SUPPLY AND INSTALL 1/4" CLEAR WIRE GLASS AND USE GLAZING TAPE TO PROTECT GLASS IN THE FRAME.	
1 EA (VERIFY - SEE SPECIAL INSTRUCTION N)	KICKPLATE:	ASSA ABLOY-ROCKWOOD	(RESTROOMS) K1050 US320 12 34 BEV, (BREAKROOM) K1050 US320 12x40 BEV	630 (Satin SS), US320	ATTACHED TO THE PUSH SIDE OF THE DOOR 1/2" ABOVE THE BOTTOM, AND IN 1" FROM BOTH RIGHT AND LEFT EDGES THE DOOR. REQUIRED FOR THE 1" ABOVE EX UNDERCUT DOOR.	
1 EA	WALL STOP:	ASSA ABLOY-ROCKWOOD	400	626 (Satin Chromium), US260	PROVIDE BACKING IN WALL.	
3 EA	SILENCERS:	ASSA ABLOY-ROCKWOOD	608-RKW	GREY	INSTALL AFTER FRAME IS PAINTED	
HARDWARE SET #4 - INTERIOR WOOD SINGLE DOOR (SINGLE OCCUPANT RESTROOM, DORMITORY HARDWARE (each opening to receive):						
QTY	PART	MANUFACTURER	PART #	FINISH	SPECIAL INSTRUCTIONS	
3 EA	HINGES:	MC KINNEY	MP/B79 (US260) 4.5" X 4.5"	626 (Satin Chromium), US260	STANDARD DUTY BALL BEARING MORTISE HINGE	
1 EA	LOCKSET (OPTION - 1A):	ASSA ABLOY ACCENTRA (YALE)	9-PB9422IN-626	626 (Satin Chromium), US260	CONDUIT FUNCTION: WITH A RED COLORED TEMPORARY INSTA KEY 7 PIN REMOVABLE CORE AND CORE CHANGING KEY.	
1 EA	IC CORE:	INSTANEY	SPIC CORE 7 PIN		RED COLORED	
1 EA	CLOSER:	CORBIN-RUSSWIN (CR)	(CR) DC6200	689 (Painted Silver)	FASTEN CLOSER BODY TO DOOR ON SWING SIDE OF DOOR WITH WOOD SCREWS (NO EX BOLTS OR PARALLEL BAR) AND JUST TO NO MORE THAN 12 INBS PULL RESISTANCE (EASY OPENING AND SLOW CLOSING).	
1 EA	KICKPLATE:	ASSA ABLOY-ROCKWOOD	K1050 US320 12 34 BEV	630 (Satin SS), US320	ATTACHED TO THE PUSH SIDE OF THE DOOR 1/2" ABOVE THE BOTTOM, AND IN 1" FROM BOTH RIGHT AND LEFT EDGES THE DOOR.	
1 EA	FLOOR STOP:	ASSA ABLOY-ROCKWOOD	481H	626 (Satin Chromium), US260	REQUIRED FOR THE 1" ABOVE EX UNDERCUT DOOR.	
3 EA	SILENCERS:	ASSA ABLOY-ROCKWOOD	608-RKW	GREY	INSTALL AFTER FRAME IS PAINTED	

HARDWARE SCHEDULE

HARDWARE SET - EXTERIOR PERIMETER HINGE DOOR (SEE EGLED ALARMED PANIC FUNCTION HARDWARE (each opening to receive):				FINISH	SPECIAL INSTRUCTIONS
QTY	PART	MANUFACTURER	PART #		
1 EA	SECURITY ASSA ABLOY-PENKO		3572P77ND	PRIME PAINT (FEL) PRIME AND PAINT WITH DOOR) SATIN STAINLESS STEEL, US32D (verify with BDF)	WELD THE SECURITY ASTIGAL TO THE ACTIVE DOOR TAKING CARE TO ACCOMMODATE THE REMAINING DOOR HARDWARE (I.E. TIME TO ALLOW SWOOP TO PASS UNDER ASTIGAL).
3 EA	HINGES: MCKINNEY		MPB91 4.5" X 4.5" NRP US32D		STANDARD COLD BAL BEARING MORTISE HINGE
1 EA	THRESHOLD: ASSA ABLOY		175A	A-MILL ALUMINUM (verify with BDF)	SET AND ANCHOR THRESHOLD IN A SOLID BED OF "DOWSIL" CONCRETE SEALANT (OR EQUAL).
1 EA	DOOR DRIP: ASSA ABLOY-PENKO		346C	C- CLEAR ANODIZED ALUMINUM (field painted)	TO BE ORDERED 4" WIDER THAN THE OVERALL DOOR OPENING AND MOUNTED TO THE WINDOW FRAME HEAD. PRIME AND PAINT TO MATCH EXTERIOR COLOR OF DOOR FRAME.
1 SET (VERIFY-SEE SPECIAL INSTRUCTION N)	WEATHER-STRIPPING: NATIONAL GUARD PRODUCTS		700N (CONTINUOUS HEAD AND BOTH LEGS)	MIL ALUMINUM	**INSTALL AFTER THRESHOLD IS INSTALLED AND DOORS HUNG, BUT BEFORE ALL OTHER DOOR HARDWARE.** MOUNT TO HEAD AND BOTH DOOR FRAME LEGS. WEATHER-STRIP TO BE CONTINUOUS AND WITHOUT GAPS, JAWLIGT, WEATHER, OR BULBS PASSING THROUGH. PANIC HARDWARE STRIKES, CLOSERS, BURGULAR CONTACTS, ETC. ARE TO MOUNT TOP OF THE WEATHERSTRIP THICK ALUMINUM BAR BODY AFTER WEATHERSTRIP IS INSTALLED.
1 EA	KICKPLATE: ASSA ABLOY-ROCKWOOD		K1050 US32D 12 34 BEV	630 (Satin SS), US32D	ATTACHED TO THE POSH SIDE OF THE DOOR 12" ABOVE THE BOTTOM AND IN 1" FROM BOTH RIGHT AND LEFT EDGES THE DOOR. INSTALL KICKPLATE AFTER DOOR IS PAINTED.
1 EA (VERIFY-SEE SPECIAL INSTRUCTION N)	ALARMED EXIT DEVICE (OPTION -6A)	DETEX	ECI - 230X - 1K78 - B6	GRAY	CONTRACTOR TO SUPPLY/INSTALL THE LOCKSET WITH A RED COLORED TEMPORARY INSTA-KIT 7-PIN REMOVABLE CORE AND CORE CHANGING KEY. BDF TO SUPPLY/INSERT PERMANENT CORES AFTER CONSTRUCTION COMPLETION DATE. INSTALL AFTER DOOR IS PAINTED.
1 EA (VERIFY-SEE SPECIAL INSTRUCTION N)	ALARMED EXIT DEVICE (OPTION -6B)	DETEX	ECI - 230X - 1DB 84" (VERIFY) B6 X 1K78	GRAY	**SUPPLY AT HIGH RISKS STORES ONLY.** CONTRACTOR TO SUPPLY/INSTALL WITH A RED COLORED TEMPORARY INSTA-KIT 7-PIN REMOVABLE CORE AND CORE CHANGING KEY. BDF TO SUPPLY/INSERT PERMANENT CORES AFTER CONSTRUCTION COMPLETION DATE. INSTALL AFTER DOOR IS PAINTED.
1 EA	IC CORE	INSTAKY	SFIC CORE 7 PIN		OPTION 6A & 8B - RED COLORED
1 EA	PULL CORE: ASSA ABLOY-ROCKWOOD		102-860V X TYPE GR 60 H/MOUNTING	620 (Satin SS), US32D	**INSTALL ON INTERIOR SIDE ONLY.** CONTRACTOR TO INSTALL THE PULL ON THE INTERIOR SIDE OF DOOR LEAT TO ALLOW STORE TEAM TO PULL DOOR SHUT FORCEFULLY TO ENSURE FULL CONTACT AND PROPER LATCHING. INSTALL VERTICALLY 4" ABOVE THE DETEX DEVICE AND 4" FROM THE DOOR EDGE.
1 EA (VERIFY-SEE SPECIAL INSTRUCTION N)	EXTERIOR PULL/TUM	DETEX	03PP	626 (Satin Chromium, US26D)	**ONLY IF EXTERIOR ACCESS IS REQUIRED BY FIRE MARSHALL ON A DETEX HARDWARE DOOR.** CONTRACTOR TO SUPPLY/INSTALL THE PULL TUM AND CYLINDER WITH A GREEN COLORED TEMPORARY INSTA-KIT 7-PIN REMOVABLE CORE AND CORE CHANGING KEY.
1 EA (VERIFY-SEE SPECIAL INSTRUCTION N)	EXTERIOR CYLINDER	KILEEN	308-26D	626 (Satin Chromium, US26D)	
1 EA	CLOSER: CORBIN-RUSSWIN (CR)	(CR)	DC6210 (PARALLEL ARM)	689 (Painted Silver)	MOUNT ON PUSH SIDE OF THE DOOR WITH PARALLEL ARM AND ADJUST TO NO MORE THAN 12 LBS PULL RESISTANCE, AND A SLOW AND SOFT CLOSING.
1 EA (VERIFY-SEE SPECIAL INSTRUCTION N)	DOOR VIEWER: ASSA ABLOY-ROCKWOOD		622DRM	DCRM (Dull Chrome) (verify with BDF)	**ONLY ON THE DOOR ADJACENT TO A DOOR BELL.** INSTALL CENTER OF THE DOOR AT 5' AFF.
1 EA (VERIFY-SEE SPECIAL INSTRUCTION N)	WALL STOP: ASSA ABLOY-ROCKWOOD		400	626 (Satin Chromium, US26D (verify with BDF)	**ONLY WHERE STOP CAN BE MOUNTED TO A SOLID WALL CONDITION** THIS IS THE PREFERRED METHOD UNLESS NO SOLID WALL WITH CONDITIONS MOUNT ON SOLID BRICKS, OR CONCRETE WALL. IF SOLID WALL IS NOT AVAILABLE THEN USE FLOOR STOP.
1 EA (VERIFY-SEE SPECIAL INSTRUCTION N)	FLOOR STOP: ASSA ABLOY-ROCKWOOD		481H	626 (Satin Chromium, US26D (verify with BDF)	**ONLY IF WALL MOUNTING CONDITION IS NOT ON A SOLID WALL** MOUNT AS CLOSE TO THE WALL AS POSSIBLE TO KEEP DOOR AND HARDWARE FROM HITTING THE WALL.
1 EA	SWEEP	ASSA ABLOY-PENKO	3452CNB TKSP8	CLEAR ALUMINUM (verify with BDF)	INSTALL AFTER DOOR IS PAINTED ON EXTERIOR.

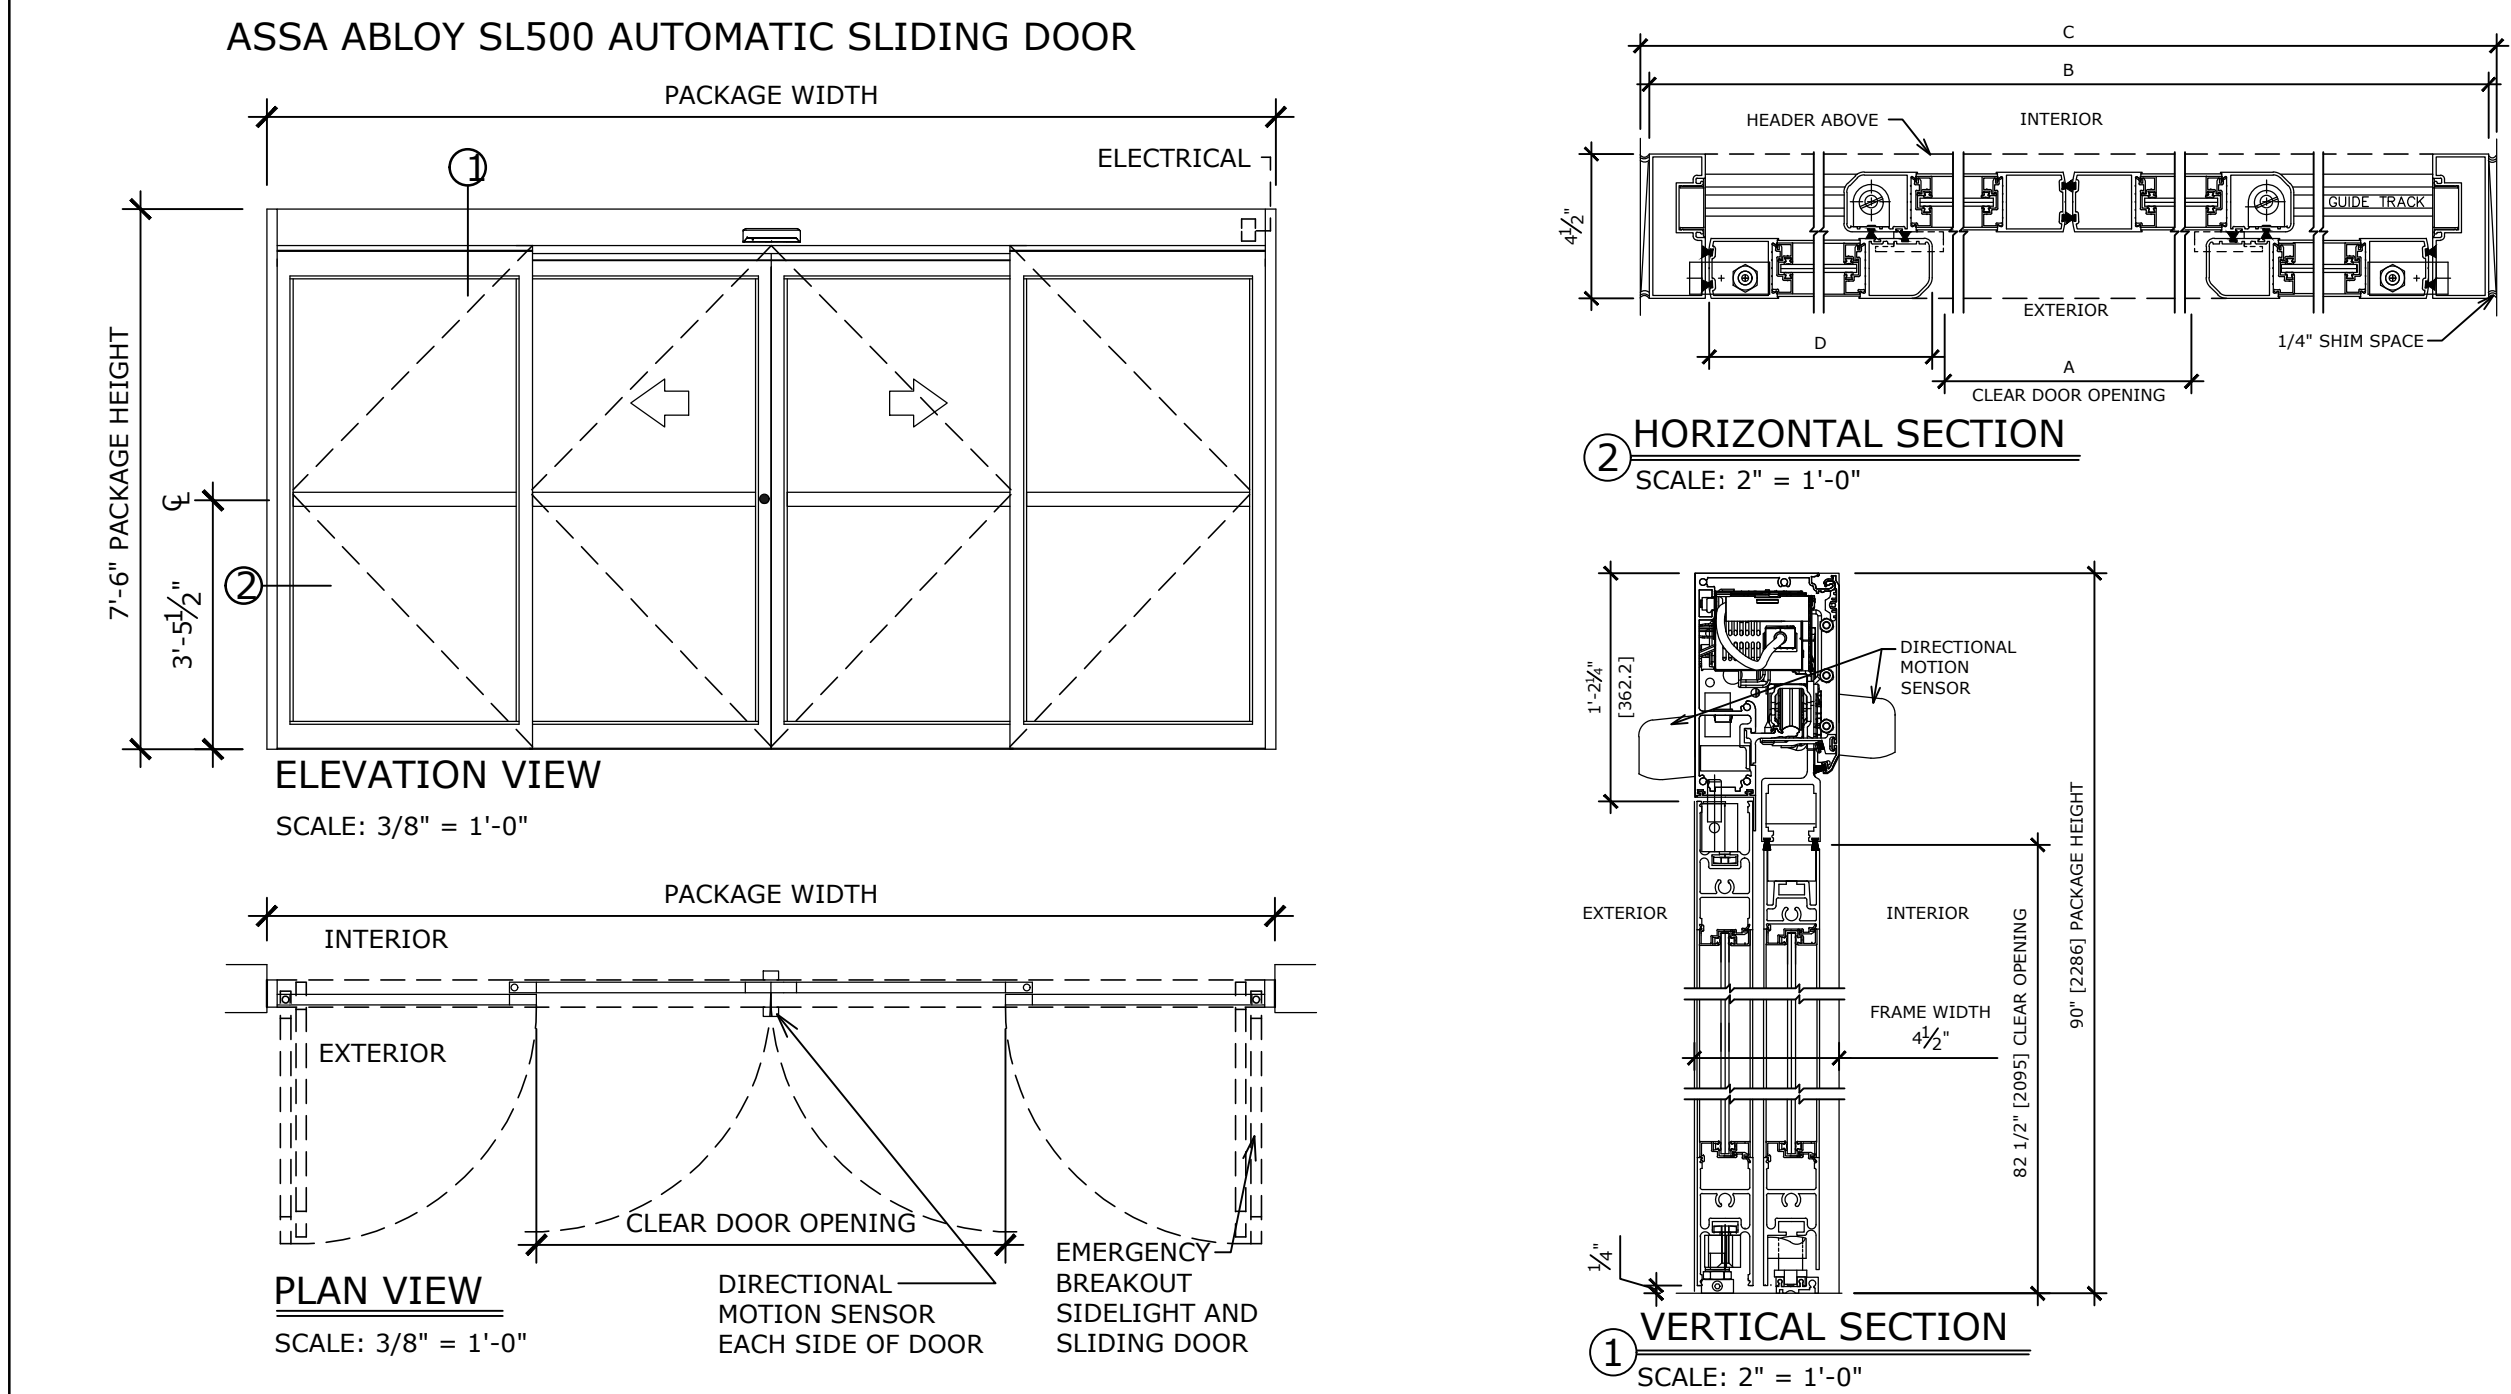

SL500 OHC	DOOR OPENING A	OVERALL FRAME WIDTH	MASONRY OPENING WIDTH	ACTIVE & SIDELITE LEAF WIDTH	NOTES:
	36" (914.4)	96" (2438.4)	96 1/2" (2451.1)	24 3/8" (619.1)	1. CONTRACTOR DEVELOP MASTER KEYING SCHEDULE IN ACCORDANCE WITH OWNER'S REQUIREMENTS. PROVIDE KEYING SCHEDULE FOR REVIEW BY BOB'S FURNITURE.
OC2-8	48" (1219.2)	120" (3048)	120 1/2" (3060.7)	30 3/8" (771.5)	2. ALL FINISH HARDWARE TO BE USED/80% FINISH. U.L.O.
OC2-10	48" (1219.2)	120" (3048)	120 1/2" (3060.7)	30 3/8" (771.5)	3. PROVIDE N.R.P. HINGES FOR ALL OUT-EXTING EXTERIOR DOORS.
OC2-12	72" (1828.8)	168" (4267.2)	168 1/2" (4238.1)	42 3/8" (1076.5)	4. ALL INTERIOR WOOD DOORS SHALL BE SOLID CORE ROTARY CUT BIRCH.
OC2-14	72" (1828.8)	168" (4267.2)	168 1/2" (4238.1)	42 3/8" (1076.5)	5. PRE-FINISH W/CLAR POLYURETHANE FINISH.
OC2-16	84" (2133.6)	192" (4878.8)	192 1/2" (4889.5)	48 3/8" (1228.7)	6. PROVIDE HANDICAP DOOR HARDWARE IN COMPLIANCE WITH THE ADA STANDARDS OF THE BUILDING CODE. TYPICAL.
KEY	84" (2133.6)	192" (4878.8)	192 1/2" (4889.5)	48 3/8" (1228.7)	7. ALL DOORS, INTERIOR AND EXTERIOR, TO HAVE 7-PIN CYLINDERS.
	84" (2133.6)	192" (4878.8)	192 1/2" (4889.5)	48 3/8" (1228.7)	8. FOR INTO ROOM SWING DOORS - FASTER CLOSER BODY TO DOOR ON OPPOSITE SIDE OF DOOR WITH WOOD SCREWS (NO SEX BOLTS) AND NO PARALLEL BAR. FOR OUT OF ROOM SWING DOORS (TYPICALLY JANITORS AND ELECTRIC) FASTER CLOSER BODY TO PARALLEL BAR ON PUSH SIDE OF DOOR WITH WOOD SCREWS (NO SEX BOLTS) WITH PARALLEL BAR. NO MORE THAN 12 LBS PULL RESISTANCE (EASY OPENING AND SOFT CLOSING).

Legend

- ☒ Door Frame - HM
- ☒ Doors -HM
- ☒ Doors -WD

CAMBURAS & THEODORE, LTD
ARCHITECTURE | ENGINEERING | INTERIORS
2454 E. Dempster St., Suite 202
Des Plaines, IL 60016
P (847) 238-1525 | F (847) 530-8130
www.camburasandtheodore.com

THESE DRAWINGS AND SPECIFICATIONS, AS INSTRUMENTS OF SERVICE, ARE AND SHALL REMAIN THE PROPERTY OF THE ARCHITECT WHETHER THE PROJECT FOR WHICH THEY ARE MADE IS EXECUTED OR NOT. THESE DRAWINGS AND SPECIFICATIONS SHALL NOT BE USED BY ANY PERSON OR ENTITY ON OTHER PROJECTS. FOR ADDITIONS TO THIS PROJECT OR COMPLETION OF THIS PROJECT-WHEN PHASED-WITHOUT THE WRITTEN CONSENT OF C + T, LTD. Copyright © 2025

BOB'S Discount Furniture.
COBB PLACE SHOPPING CENTER
840 ERNEST W BARRETT PARKWAY NW, SUITE 100
KENNESAW, GA 30144

REVISION DATES												
TYPE												
NO.	DATE											
ISSUE DATES												
TYPE										DATE		
PERMIT/CONSTRUCTION SET										05/01/2026		
DRAWN BY												
CHECKED BY												
PROJECT NUMBER												
25-91018												
DATE												
05/01/2026												
SHEET TITLE												
DOOR SCHEDULE												
& NOTES												
SHEET NUMBER												
A8.1												

