

3

TYPICAL S.C.C.P. CORNER DETAIL

SCALE: 1/2" = 1'-0"

2

TYP. S.C.C.P. MITERED CORNER

SCALE: 1/2" = 1'-0"

GENERAL NOTES

CONCRETE ROOF OF ELECTRICAL PLANTS.
WITH ACCESS LADDER FROM ELECTRICAL ROOF BELOW. G.C. TO UCTURE, PAINTED SAFETY ED PLANS AND ROOF PLAN.

OUR RATED

OUR RATED

DETAILS 4, 12 & 13 ON A-401

SLOPE AWAY FROM BUILDING AT

DOWNSPOUTS WITH KYNAR

N SOFFIT ABOVE

- SEE PLUMBING

DE 6" PVC CLEANOUTS AT 80'-0"

PED TO HUB DRAIN OR THRU RAMP TO TRUCK COURT. PROVIDE BIRD

A.F.F. - SEE STRUCTURAL

- BUILDING TO BE 36' CLEAR JUST PAST THE FIRST COLUMN LINE IN FROM THE DOCK WALL.
- SLAB CONTROL JOINTS TO BE SAWCUT AND NOT TO EXCEED 15'-0" ON CENTER. SEE STRUCTURAL DRAWINGS FOR FLOOR SLAB CONTROL JOINTS. PROVIDE ALTERNATE PRICE FOR PNA FDS DOWEL BASKETS AT SLAB CONTROL JOINTS IN SPEED BAY ONLY - SIZED AND SPACED PER AISC RECOMMENDATIONS - SEE STRUCTURAL DRAWINGS.
- SLAB CONSTRUCTION JOINTS TO HAVE DIAMOND DOWELS SIZED AND SPACED PER AISC RECOMMENDATIONS - SEE STRUCTURAL DRAWINGS. CAULK AROUND COLUMN DIAMOND/SLEEVE.
- SLAB WILL BE CURED WITH A WATER-BASED DISSIPATIVE CURING COMPOUND AND WILL RECEIVE TWO COATS OF SONNEBORNE LAPIDOLITH FORMULA FLOOR HARDENER.
- SLAB ON GRADE WILL BE PRE-TREATED WITH TERMITICIDE.
- 10-MIL CLASS "A" VAPOR BARRIER TO BE PROVIDED BELOW THE SLAB ON GRADE THROUGHOUT. ALL SEAMS AND PENETRATIONS TO BE SEALED AND TAPED.
- 7" THICK UNREINFORCED, 4,000 PSI CONCRETE SLAB BEARING ON 8" GAB. VERIFY SUB-GRADE WITH GEOTECH REPORT. SLAB TO RECEIVE HARD TROWEL FINISH AND LASER SMOOTH SHALL BE UTILIZED TO ATTAIN MINIMUM LOCAL & OVERALL SLAB TOLERANCE OF FF 45/FL 35. PROVIDE ALTERNATE PRICE FOR SOIL CEMENT ON BUILDING PAD LOG GAB, USING AN APPLICATION OF 40LBS FOR 8 INCH SECTION WITH 4" LAYER OF GAB ON TOP OF SOIL CEMENT IN AREAS DESIGNATED AS POTENTIAL OFFICE AREAS.
- PROVIDE A ESFR SPRINKLER SLAB THROUGHOUT.
- PROVIDE PORTABLE FIRE EXTINGUISHERS OF THE QUANTITY AND AT THE LOCATIONS AS INDICATED OR AS REQUIRED BY THE AUTHORITY HAVING JURISDICTION. EXTINGUISHERS SHALL BE EQUAL TO J.L. INDUSTRIES COSMIC 10B, 10 POUND, 4A-80BC, TO BE COORDINATED WITH OWNERS LAYOUT.
- METAL ROOF DECK SHALL BE 1-1/2" TYPE "B" WIDE RIB DECKING SHOP PRIMED WHITE ON THE UNDERSIDE/INSIDE FACE - SEE STRUCTURAL DRAWINGS.
- RACKING, FLOOR STORAGE AND EQUIPMENT BY OTHERS.
- SEE ELEVATIONS FOR GLASS SCHEDULE.
- ALL BOLLARDS TO BE PAINTED SAFETY YELLOW. (PROVIDE BOLLARDS AT ALL DRIVE-IN OVERHEAD DOOR JAMBS, FIRE PROTECTION RISERS, ELECTRICAL TRANSFORMERS AND EXPOSED ELECTRICAL PANELS).
- ALL BOLLARDS SHALL BE 6" O.D. SCHEDULE 80 STEEL PIPE SET MINIMUM 2'-0" DEEP IN 2'-0" DIAMETER CONCRETE FOOTING WITH PIPE EXTENDED 4'-0" ABOVE PAVING OR FLOOR. FILL PIPE WITH CONCRETE AND CAP WITH PRECAST CONCRETE DOME TOP - FOOTING TO BE IN SLOTTED.
- ROOF ASSEMBLY: SINGLE PLY 45 MIL WHITE TPO MEMBRANE SYSTEM MECHANICALLY FASTENED OVER R-20 ROOF INSULATION (TWO LAYERS STAGGERED) OVER 1-1/2" METAL DECK, 15-YEAR NDL WARRANTY, R-25 ROOF INSULATION (TWO LAYERS STAGGERED) OVER OFFICE AREA.
- ALL STAIRS AND RAILINGS TO BE GALVANIZED. ALL MISC. STEEL TO BE HD GALVANIZED FOR EXTERIOR APPLICATIONS. SHOP DE-BURR UNDERSIDE OF HANDRAILS. USE GALVANIZED PAINT TO TOUCH-UP FIELD WELDING AND SCRATCHES.
- ALL SITE CAST CONCRETE PANEL WIDTHS ARE TO CENTERLINE OF CONCRETE PANEL VERTICAL JOINT U.N.O.
- ALL TILT WALL PANELS SHALL BE CAULKED TO FULL HEIGHT, BOTH SIDES, WITH TREMCO DYMERIC POLYURETHANE SEALANT OR EQUAL WITH BACKER ROD BEHIND THE CAULK.
- (EXTERIOR) ALL S.C.C.P. SHALL BE PRIMED WITH PITTSBURGH PAINTS PERMA-CRETE INTERIOR/EXTERIOR ALKAL RESISTANT PRIMER AND RECEIVE ONE COAT OF PITTSBURGH PAINTS PERMA-CRETE ACRYLIC MEDIUM TEXTURE COATING WITH ONE COAT OF PITTSBURGH PAINTS PERMA-CRETE HIGH BUILD 100% THERM ACRYLIC FLAT ACENT STRIPING. SEE ELEVATIONS.
- (INTERIOR) ALL S.C.C.P. PANELS WILL BE HARD TROWEL FINISHED WITH GROUTED AND SMOOTHED PICK AND BRACE POINTS. PANELS SHALL RECEIVE ONE (1) COAT OF ACRYLIC LATEX FLAT ENAMEL PAINT - PITTSBURGH PAINTS PPG1001-1 DELICATE WHITE
- PERSONNEL DOORS AND MISC. METALS SHALL RECEIVE ONE (1) PRIMER COAT AND TWO (2) FINISH COATS OF ENAMEL PROVIDE FIRE DEPARTMENT ACCESS SIGNAGE PER DETAIL 9/A-002 AT EACH PERSONNEL DOOR.
- TEST AND CONFIRM COMPLIANCE WITH THE INTERNATIONAL FIRE CODE SECTION 510 FOR EMERGENCY RESPONDER RADIO COVERAGE. IF REQUIRED BY TEST, PROVIDE AND INSTALL AN APPROVED SYSTEM BY A FCC LICENSED RADIO CONTRACTOR.
- ALL MASONRY ROOMS TO RECEIVE ONE (1) COAT OF BLOCK FILL AND ONE (1) COAT OF ACRYLIC LATEX WHITE SEMI-GLOSS ENAMEL PAINT.
- ALL INTERIOR COLUMNS SHALL BE PRIMED AND RECEIVE ONE (1) COAT OF ALKYO SEMI-GLOSS SAFETY YELLOW PAINT TO 12" A.F.F. COLUMNS WITH FIRE EXTINGUISHERS MOUNTED TO THEM SHALL RECEIVE A 2'-0" RED STRIPE AT 28' A.F.F. (OR AT HEIGHT DESIGNATED BY THE LOCAL FIRE MARSHAL). TOP OF THE RED STRIPE / YELLOW PAINT UP TO THE JOISTS / GIRDERS SHALL RECEIVE ONE (1) COAT OF ALKYO WHITE SEMI-GLOSS PAINT.
- PROVIDE 1.5 AIR CHANGES PER HOUR USING UPPLAST FANS AND INTERLOCKED LOUVERS - SEE ELEVATIONS AND MECHANICAL DRAWINGS.
- ALL INTERIOR COLUMN SLEEVES & BLOCKOUTS SHALL BE CAULKED AROUND THE BASE OF THE COLUMNS.



FILE PATH: Autodesk Doss/2801014 - Crow - Cass White/2801014 - Crow - CassWhite.rvt

SHEET NAME: EXTERIOR ELEVATIONS - OPTION 01 SHEET NUMBER: A-201 PROJECT NAME: CASS WHITE ROAD

GLASS SCHEDULE

A	1" INSULATED INNER PANE 1/4" OUTER PANE 1/4"	B	1" INSULATED INNER PANE 1/4" OUTER PANE 1/4"	C	1" INSULATED INNER PANE 1/4" OUTER PANE 1/4"
	HEAT STRENGTHENED		HEAT STRENGTHENED		HEAT STRENGTHENED
	GUARDIAN GLASS		GUARDIAN GLASS		GUARDIAN GLASS
	STYLE: SUNGUARD SN 88 COLOR: GRAY-CLEAR		STYLE: SUNGUARD SN 88 COLOR: GRAY-CLEAR		STYLE: SUNGUARD SN 88 WITH DECO HT

Legend

Exterior Painting-Til... 57,727.51 SF

EXTERIOR FINISH SCHEDULE


101	EXTERIOR TEXTURE COATING: PAINTED CONCRETE PITTSBURGH PAINTS PERMA-CRETE ACRYLIC MEDIUM TEXTURE. COLOR: TBD	COLOR LEGEND SEE ELEVATION	106	JOINT SEALER: ALUM. STOREFRONT TREMCO DYMERIC 240FC OR EQUAL COLOR: ANODIZED ALUMINUM
102	EXTERIOR TEXTURE COATING: PAINTED CONCRETE PITTSBURGH PAINTS PERMA-CRETE ACRYLIC MEDIUM TEXTURE. COLOR: TBD	COLOR LEGEND SEE ELEVATION	107	JOINT SEALER: S.C.P. JOINTS MASTERSEAL NP-2 POLYURETHANE OR EQUAL COLOR: TBD
103	EXTERIOR TEXTURE COATING: PAINTED CONCRETE PITTSBURGH PAINTS PERMA-CRETE ACRYLIC MEDIUM TEXTURE. COLOR: TBD	COLOR LEGEND SEE ELEVATION	108	EXPOSED METAL DOORS & FRAMES COLOR: PAINTED TO MATCH ADJACENT
	AL ITER, COPING, AND DOWNSPOUTS - TBD		109	PRE-ENGINEERED METAL CANOPY WITH 4mm ACM FASCIA AND 0.05" FASCIA GUTTER COLOR: REYNOLDS - TBD
	FRONT/CURTAIN WALL D BY KAWNEER ODIZED		110	PRE-ENGINEERED BULLNOSE CANOPY COLOR: PAC-CLAD - TBD

GENERAL NOTES

1. ALL GLASS TO BE TYPE "A" U.N.O. ALL GLASS IN DOORS TO BE TEMPERED.
2. ALL GLASS WITHIN 2' OF DOOR SWING TO BE TEMPERED.
3. KAWNEER TRI-FAB 451 BASIS OF DESIGN FOR STOREFRONT.
4. STOREFRONT SYSTEMS TO BE DESIGNED TO MEET ALL LOCAL AND DESIGN LOADS. SEE STRUCTURAL DRAWINGS FOR DESIGN LOAD REQUIREMENTS.
5. EXTERIOR WALL PACKS ARE INCLUDED - SEE ELECTRICAL DRAWINGS FOR LOCATIONS.
6. REVEALS SHALL WRAP EXPOSED PANEL EDGES AND EXPOSED BACK SIDES U.N.O.


KEYNOTES

- E1 CONCRETE SERVICE RAMP, SEE 12/A-401
- E2 STAIR AND GUARDRAIL, TYP. SEE 6/A-401, 8/A-401, 10/A-401
- E3 DOCK BUMPER - SEE WALL SECTIONS
- E4 PIPE DOWNSPOUTS THRU RAMP TO TRUCK COURT. PROVIDE BIRD SCREEN AT RAMP WALL
- E5 LOUVER - SEE MECHANICAL DRAWINGS
- E6 LED WALL PACK - SEE ELECTRICAL DRAWINGS

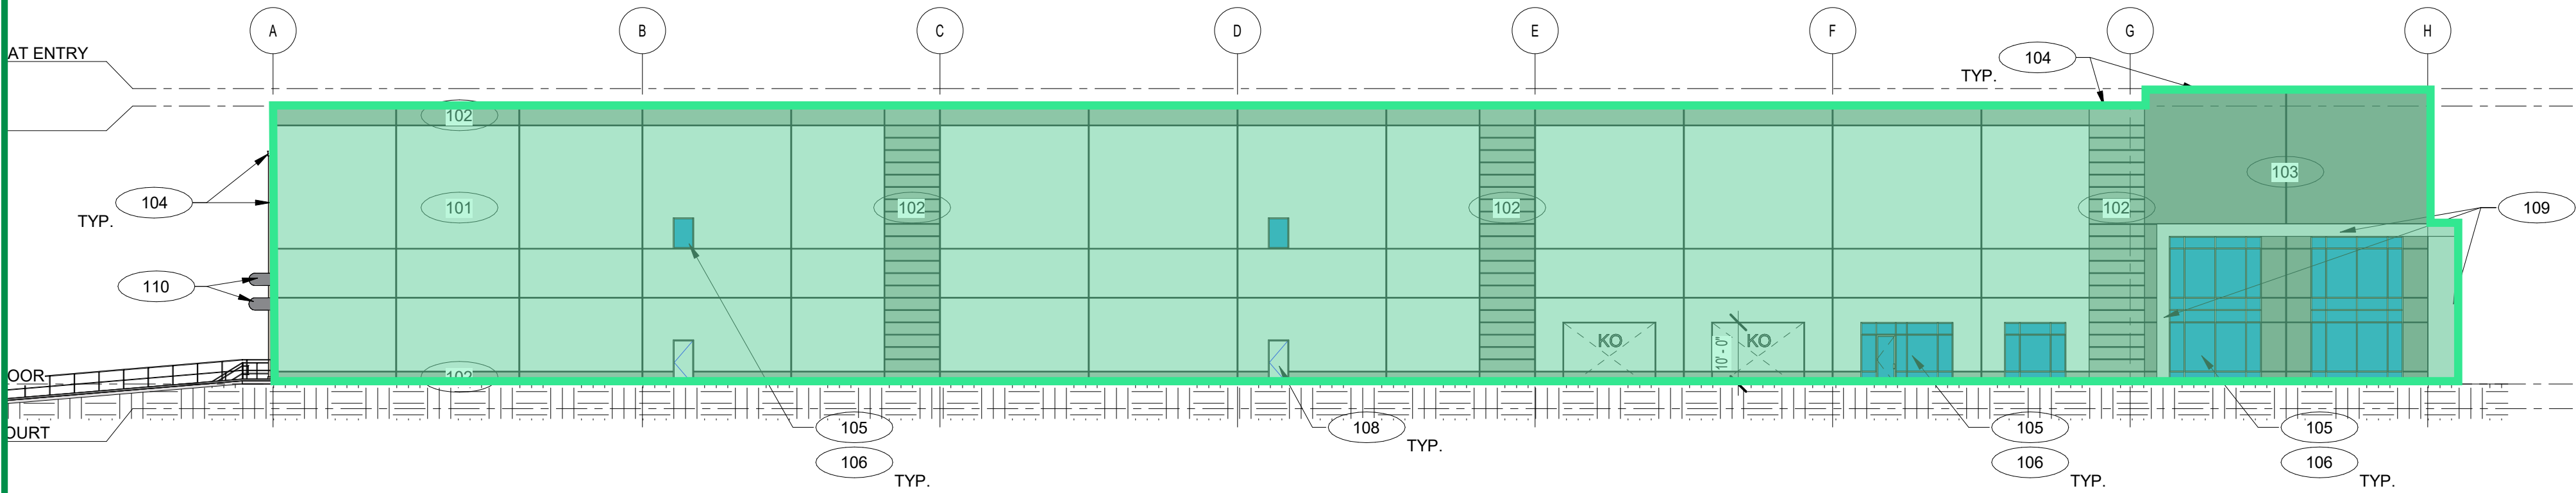


4 OVERALL WEST ELEVATION

SCALE: 1" = 20'-0"

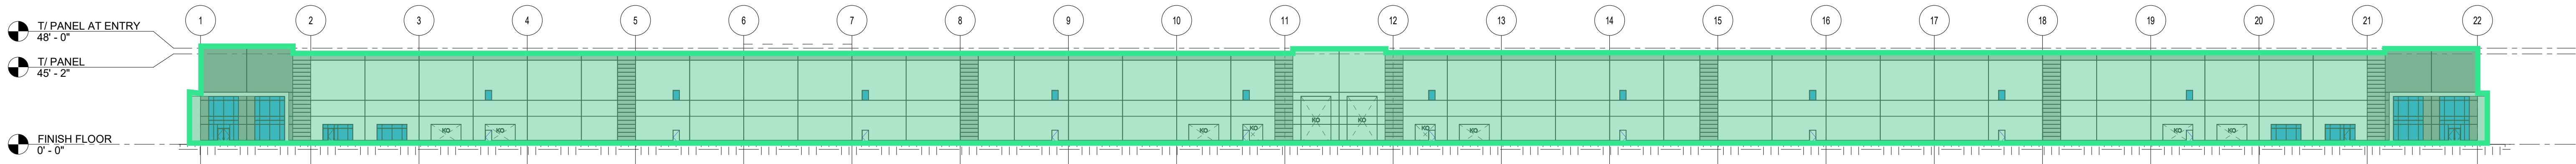


3 OVERALL SOUTH ELEVATION

SCALE: 1" = 40'-0"

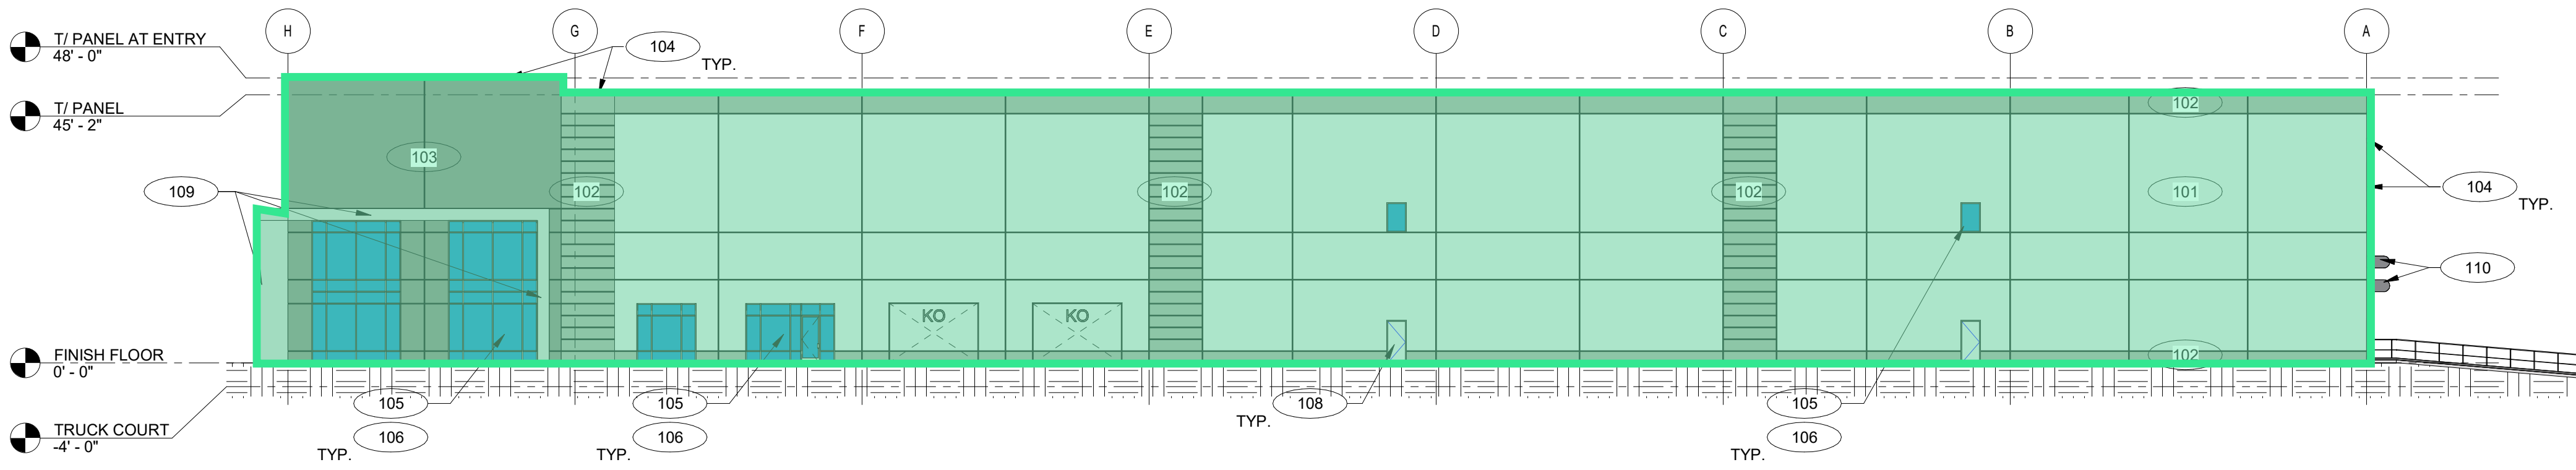


2 OVERALL EAST ELEVATION

SCALE: 1" = 20'-0"

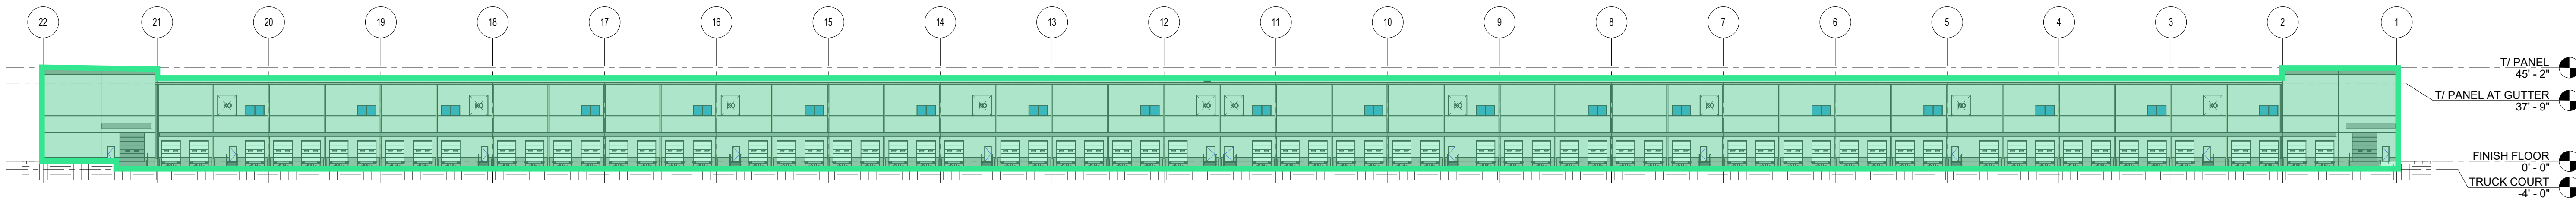

1 OVERALL NORTH ELEVATION

SCALE: 1" = 40'-0"

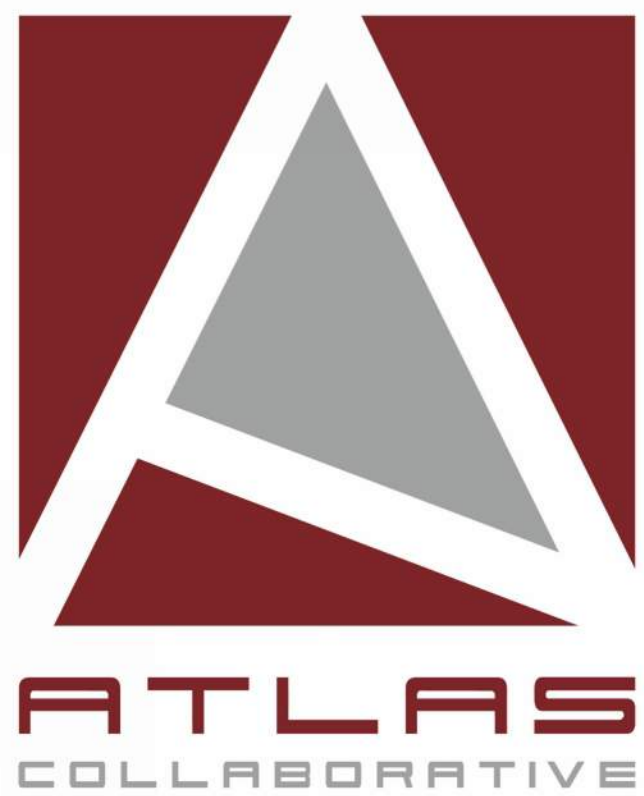

Crow Holdings
INDUSTRIAL

CASS WHITE ROAD

BARTOW COUNTY, GEORGIA

©2025, Atlas Collaborative LLC. These drawings are protected by the copyright laws of the United States. These drawings or any part thereof may not be used for any purpose or reproduced in any form or by any means without the written consent of Atlas Collaborative, LLC.

Print Record

23 FEBRUARY 2025	PLAN REVIEW
04 MARCH 2025	DESIGN REVIEW
16 MARCH 2025	DESIGN REVIEW
02 APRIL 2025	EXTERIOR OPTIONS
03 APRIL 2025	60% DESIGN REVIEW
24 APRIL 2025	95% DESIGN REVIEW

Revisions

Issue Date 04/24/2025	Job No. 2801014
--------------------------	--------------------







Sheet Title

EXTERIOR ELEVATIONS -
OPTION 01

Sheet No.

A-201

NOT ISSUED FOR CONSTRUCTION

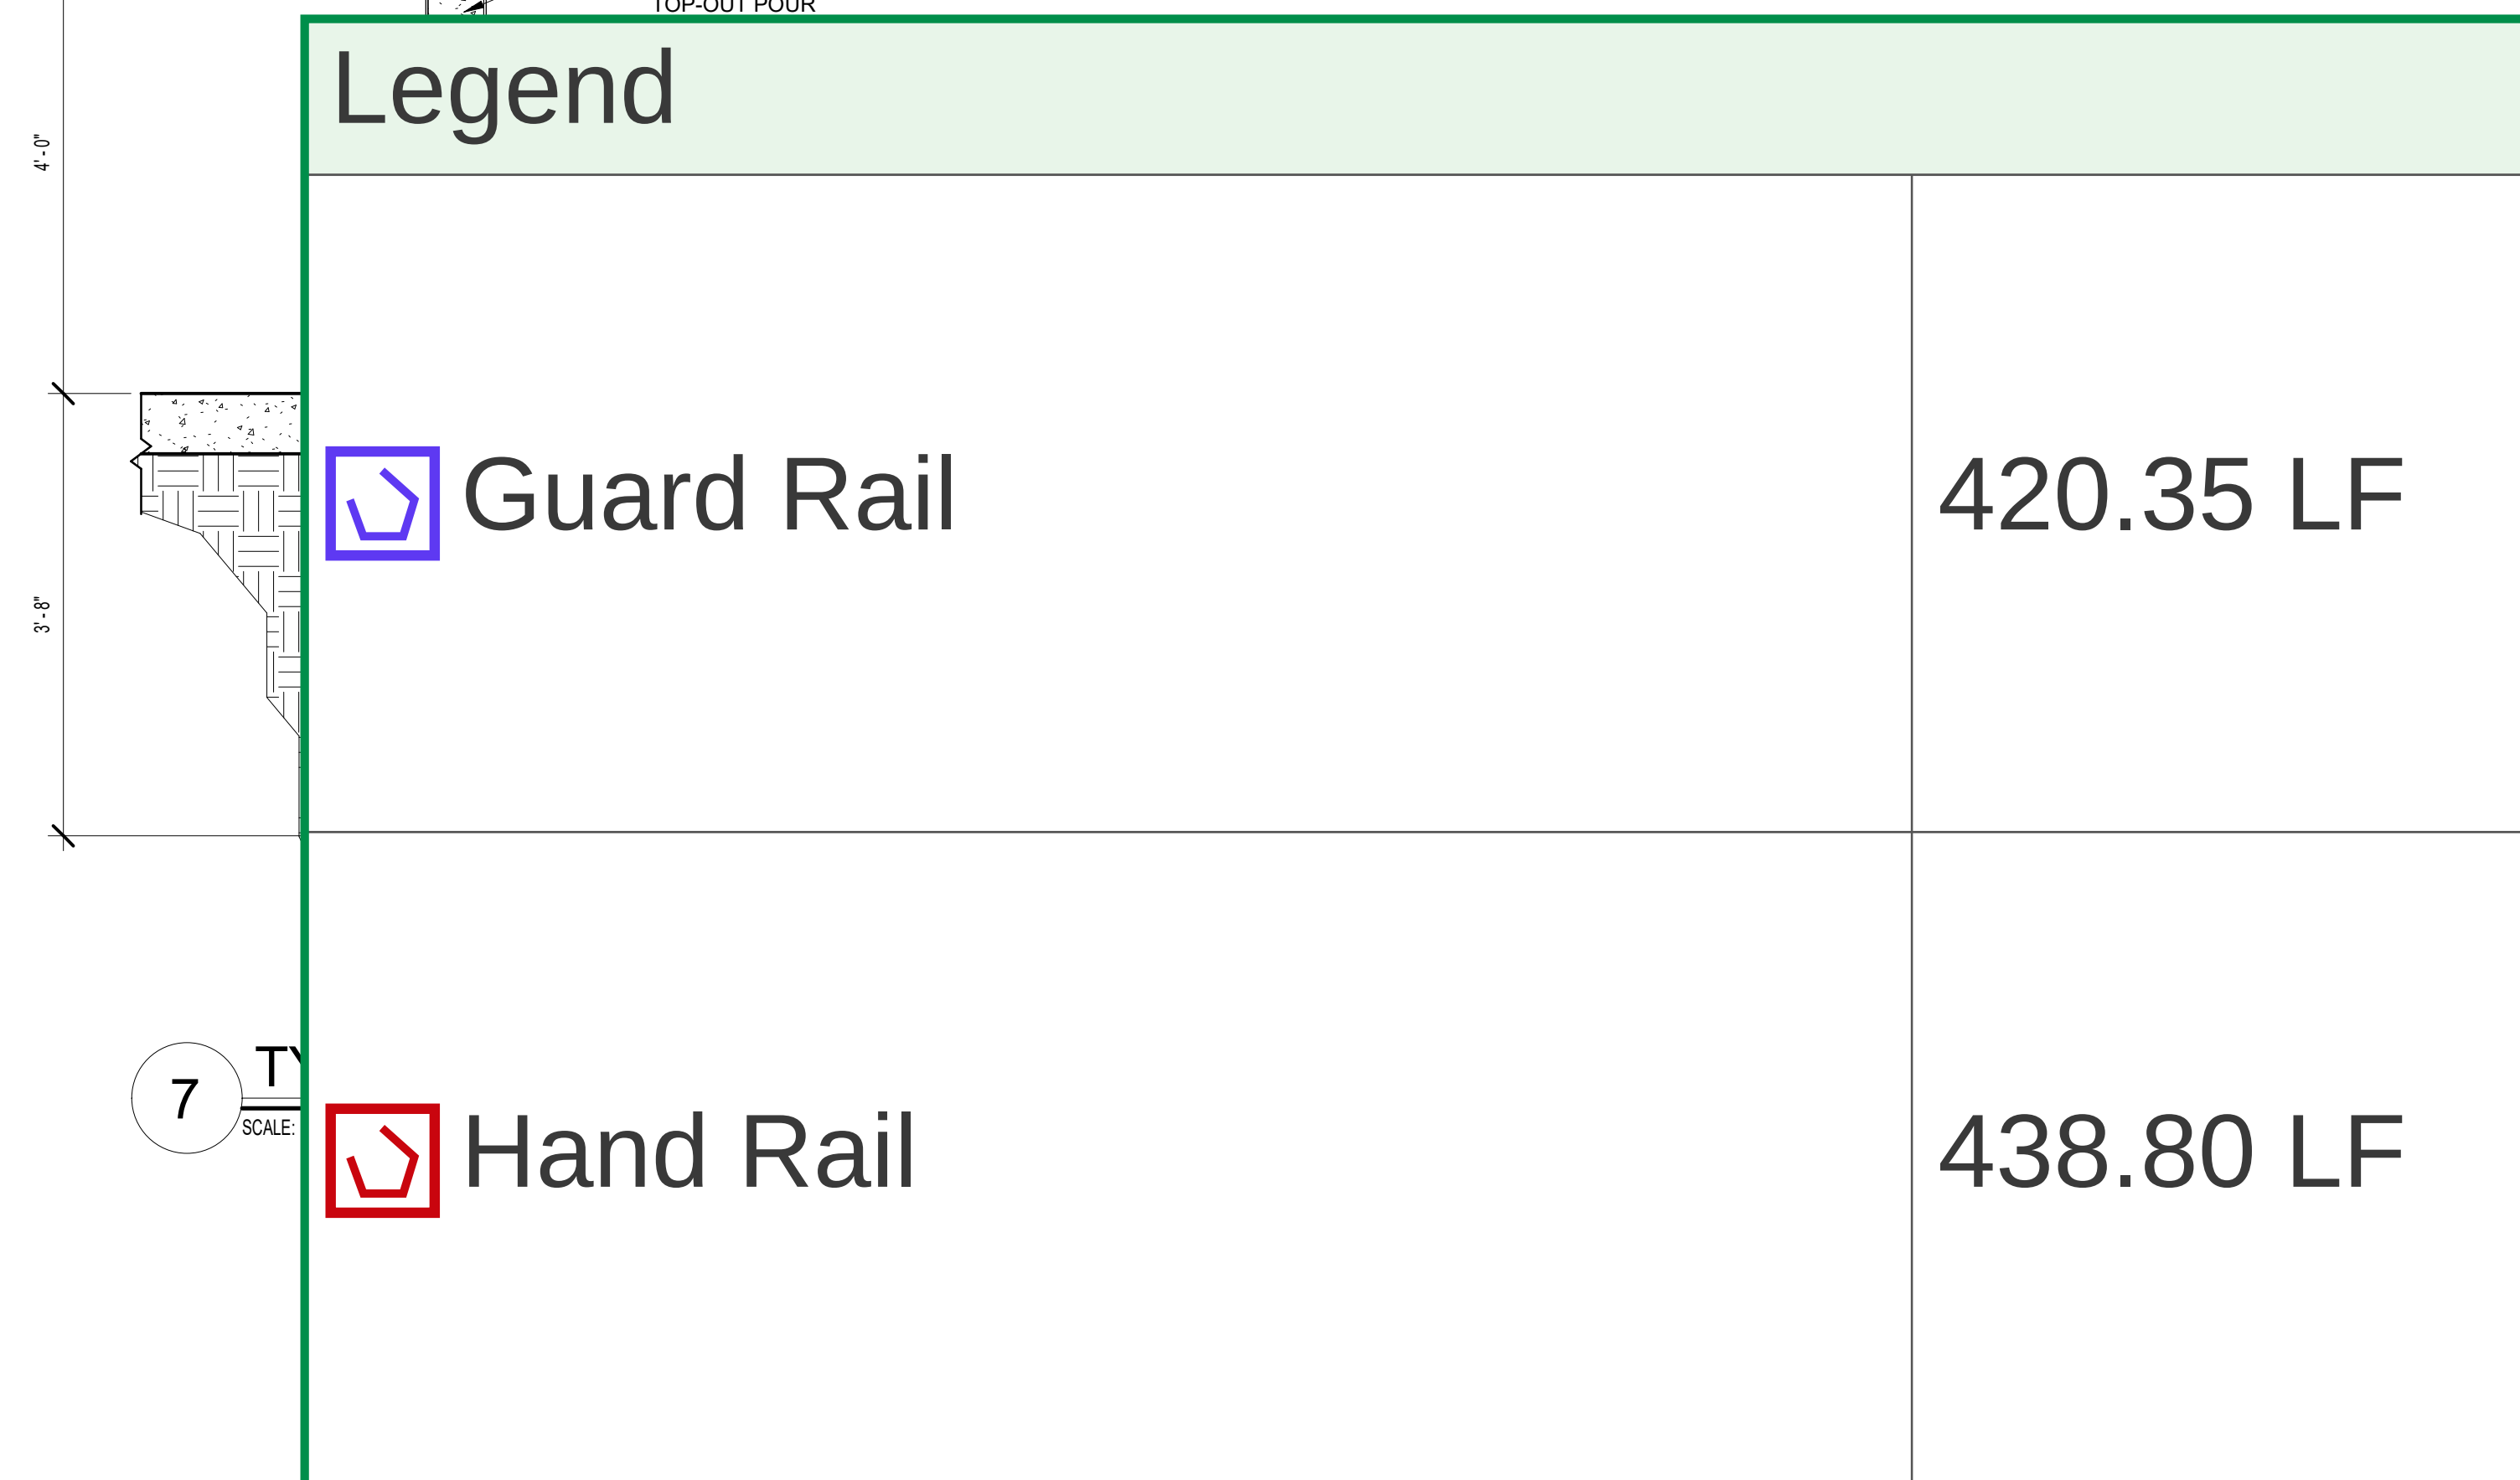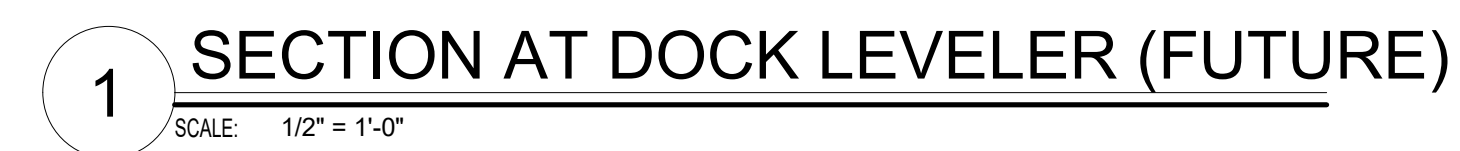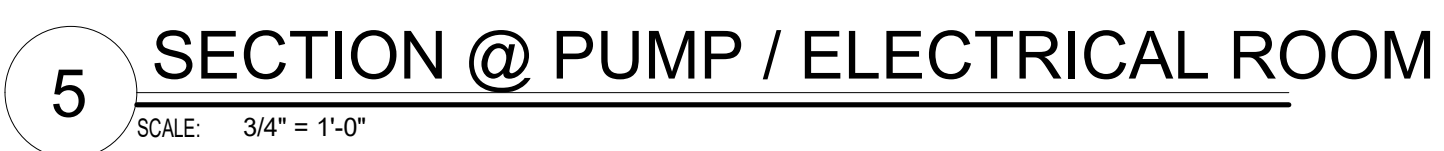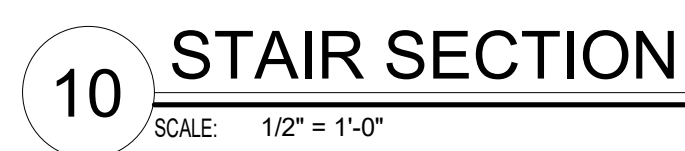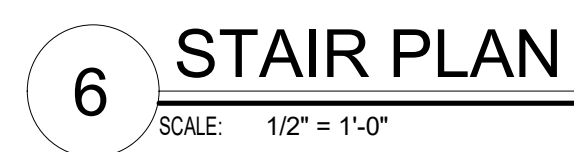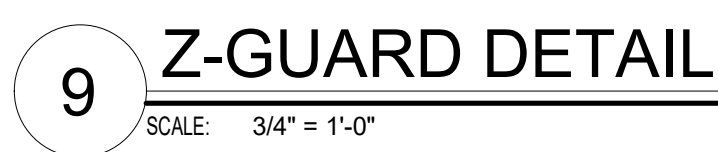

CASS WHITE ROAD

BARTOW COUNTY, GEORGIA

©2026, Atlas Collaborative LLC. These drawings are protected by the copyright laws of the United States. These drawings or any part thereof may not be used for any purpose or reproduced in any form or by any means without the written consent of Atlas Collaborative, LLC.

<i>Print Record</i>	
23 FEBRUARY 2026	PLAN REVIEW
04 MARCH 2026	DESIGN REVIEW
16 MARCH 2026	DESIGN REVIEW
02 APRIL 2026	EXTERIOR OPTIONS
03 APRIL 2026	60% DESIGN REVIEW
24 APRIL 2026	95% DESIGN REVIEW

[illegible]

Issue Date	Job No.
04/24/2026	2601014

Sheet Title

MISC. DETAILS

Sheet No. _____

A-401

NOT ISSUED FOR CONSTRUCTION

GENERAL DOOR NOTES:

- OVERHEAD AND PERSONNEL DOORS AND FRAMES TO BE DESIGNED TO MEET ALL LOCAL AND DESIGN LOADS. SEE STRUCTURAL DRAWINGS FOR DESIGN LOAD REQUIREMENTS.

WAREHOUSE DOOR HARDWARE:

ALL HARDWARE TO BE DULL CHROME FINISH (626D) OF SERIES "AL" COMMERCIAL QUALITY SCHLAGE (BEST OR EQUAL). ALL DOOR HANDLES TO BE LEVER DESIGN. ALL HINGES AND LATCHES SHALL BE STEEL WITH CHROME BRUSHED FINISH AND ALL CLOSERS SHALL BE ALUMINUM.

HW1 - SCHLAGE (OR EQUAL) HINGES, LEVER HANDLE, EXTERIOR - LOCKSET, INTERIOR - PANIC HARDWARE - CRASH BAR, AUTOMATIC CLOSER, EXTERIOR LOCK GUARD, 3" EYEBROW DRIP GUARD, WEATHERSTRIPPING, DOOR SWEEP AND ADA BUMPER THRESHOLD

HW2 - SCHLAGE (OR EQUAL) HINGES, LEVER HANDLE, EXTERIOR - LOCKSET, INTERIOR - PANIC HARDWARE - CRASH BAR, AUTOMATIC CLOSER, SMOKE SEAL, DOOR SWEEP AND ADA BUMPER THRESHOLD

HW3 - SCHLAGE (OR EQUAL) HINGES, LEVER HANDLE, EXTERIOR - LOCKSET, INTERIOR - PANIC HARDWARE - CRASH BAR, AUTOMATIC CLOSER, SMOKE SEAL, DOOR SWEEP AND ADA BUMPER THRESHOLD

HW4 - INCLUDES STOREFRONT ENTRY LOCKSET, WEATHERSTRIPPING, ADA BUMPER THRESHOLD AND FLOOR STRIP

WAREHOUSE DOOR NOTES:

NOTE 1 - (EXTERIOR DOORS) 16 GA. HOLLOW METAL DOORS IN 16 GA. WELDED HOLLOW METAL FRAMES ARE INCLUDED FOR EGRESS.

- PERSONNEL DOORS AND MISC. METALS SHALL RECEIVE ONE (1) PRIMER COAT AND TWO (2) FINISH COATS OF ALKYD ENAMEL.

NOTE 2 - (INTERIOR DOORS) 16 GA. HOLLOW METAL DOORS IN 16 GA. WELDED HOLLOW METAL FRAMES ARE INCLUDED FOR EGRESS.

- PERSONNEL DOORS AND MISC. METALS SHALL RECEIVE ONE (1) PRIMER COAT AND ONE (1) FINISH COAT OF ALKYD ENAMEL.

NOTE 3 - 24 GAUGE ACTUAL UNINSULATED, SECTIONAL, MANUALLY OPERATED, DOCK-HIGH, VERTICAL LIFT OVERHEAD DOORS WITH TWO VISION PANELS.

- DOORS SHALL BE INSTALLED ON A 3" VERTICAL TRACK WITH 25,000 CYCLE SPRINGS, WEATHERSTRIPPING, CLOSURE STEP, PROTECTED WITH Z-GUARDS AND A SLIDE LOCK MOUNTED ABOVE 48" A.F.F. TO CLEAR Z-GUARD.

NOTE 4 - 24 GAUGE ACTUAL UNINSULATED, SECTIONAL, MOTOR OPERATED, DRIVE-IN, VERTICAL LIFT OVERHEAD DOORS WITH TWO VISION PANELS.

- DOORS SHALL BE INSTALLED ON A 3" VERTICAL TRACK WITH 25,000 CYCLE SPRINGS, WEATHERSTRIPPING, PROTECTED WITH BOLLARDS AND A SLIDE LOCK MOUNTED ABOVE 48" A.F.F.

ABBREVIATIONS:

- | 1. | DOOR CONSTRUCTION: | 2. | FACING AND FINISH: | 3. | DOOR FRAME CONSTRUCTION: | 4. | OTHER: |
|----|--|---|--------------------|---|--------------------------|---|--------|
| | HC = HOLLOW CORE
SC = SOLID CORE
HM = HOLLOW METAL
IM = INSULATED METAL
AL = ALUMINUM & GLASS
STL = STEEL | PF = PRE-FINISHED
ST = STAIN
PT = PAINT
AN = ANODIZED ALUMINUM
FAC = FACTORY FINISH | | HM = HOLLOW METAL
AL = EXTRUDED ALUMINUM
EXT = EXISTING FRAME | | (X) = EXTERIOR DOOR & FRAME
(T) = TEMPERED GLASS PER SPECS.
(*) = CONCEALED HANDICAP OPERATOR | |



FRAMES

2 DOOR & FRAME TYPES

SCALE: 1/4" = 1'-0"



SCALE: 1 1/2" = 1'-0"

CASS WHITE ROAD

BARTOW COUNTY, GEORGIA

©2026, Atlas Collaborative LLC. These drawings are protected by the copyright laws of the United States. These drawings or any part thereof may not be used for any purpose or reproduced in any form or by any means without the written consent of Atlas Collaborative, LLC.

[Print Record](#)

23 FEBRUARY 2026	PLAN REVIEW
04 MARCH 2026	DESIGN REVIEW
16 MARCH 2026	DESIGN REVIEW
02 APRIL 2026	EXTERIOR OPTIONS
03 APRIL 2026	60% DESIGN REVIEW
24 APRIL 2026	95% DESIGN REVIEW

Revisions

Issue Date	Job No.
04/24/2026	2601014

Sheet Title

DOOR SCHEDULES, FRAMES & DETAILS

Sheet No

A-601

NOT ISSUED FOR CONSTRUCTION